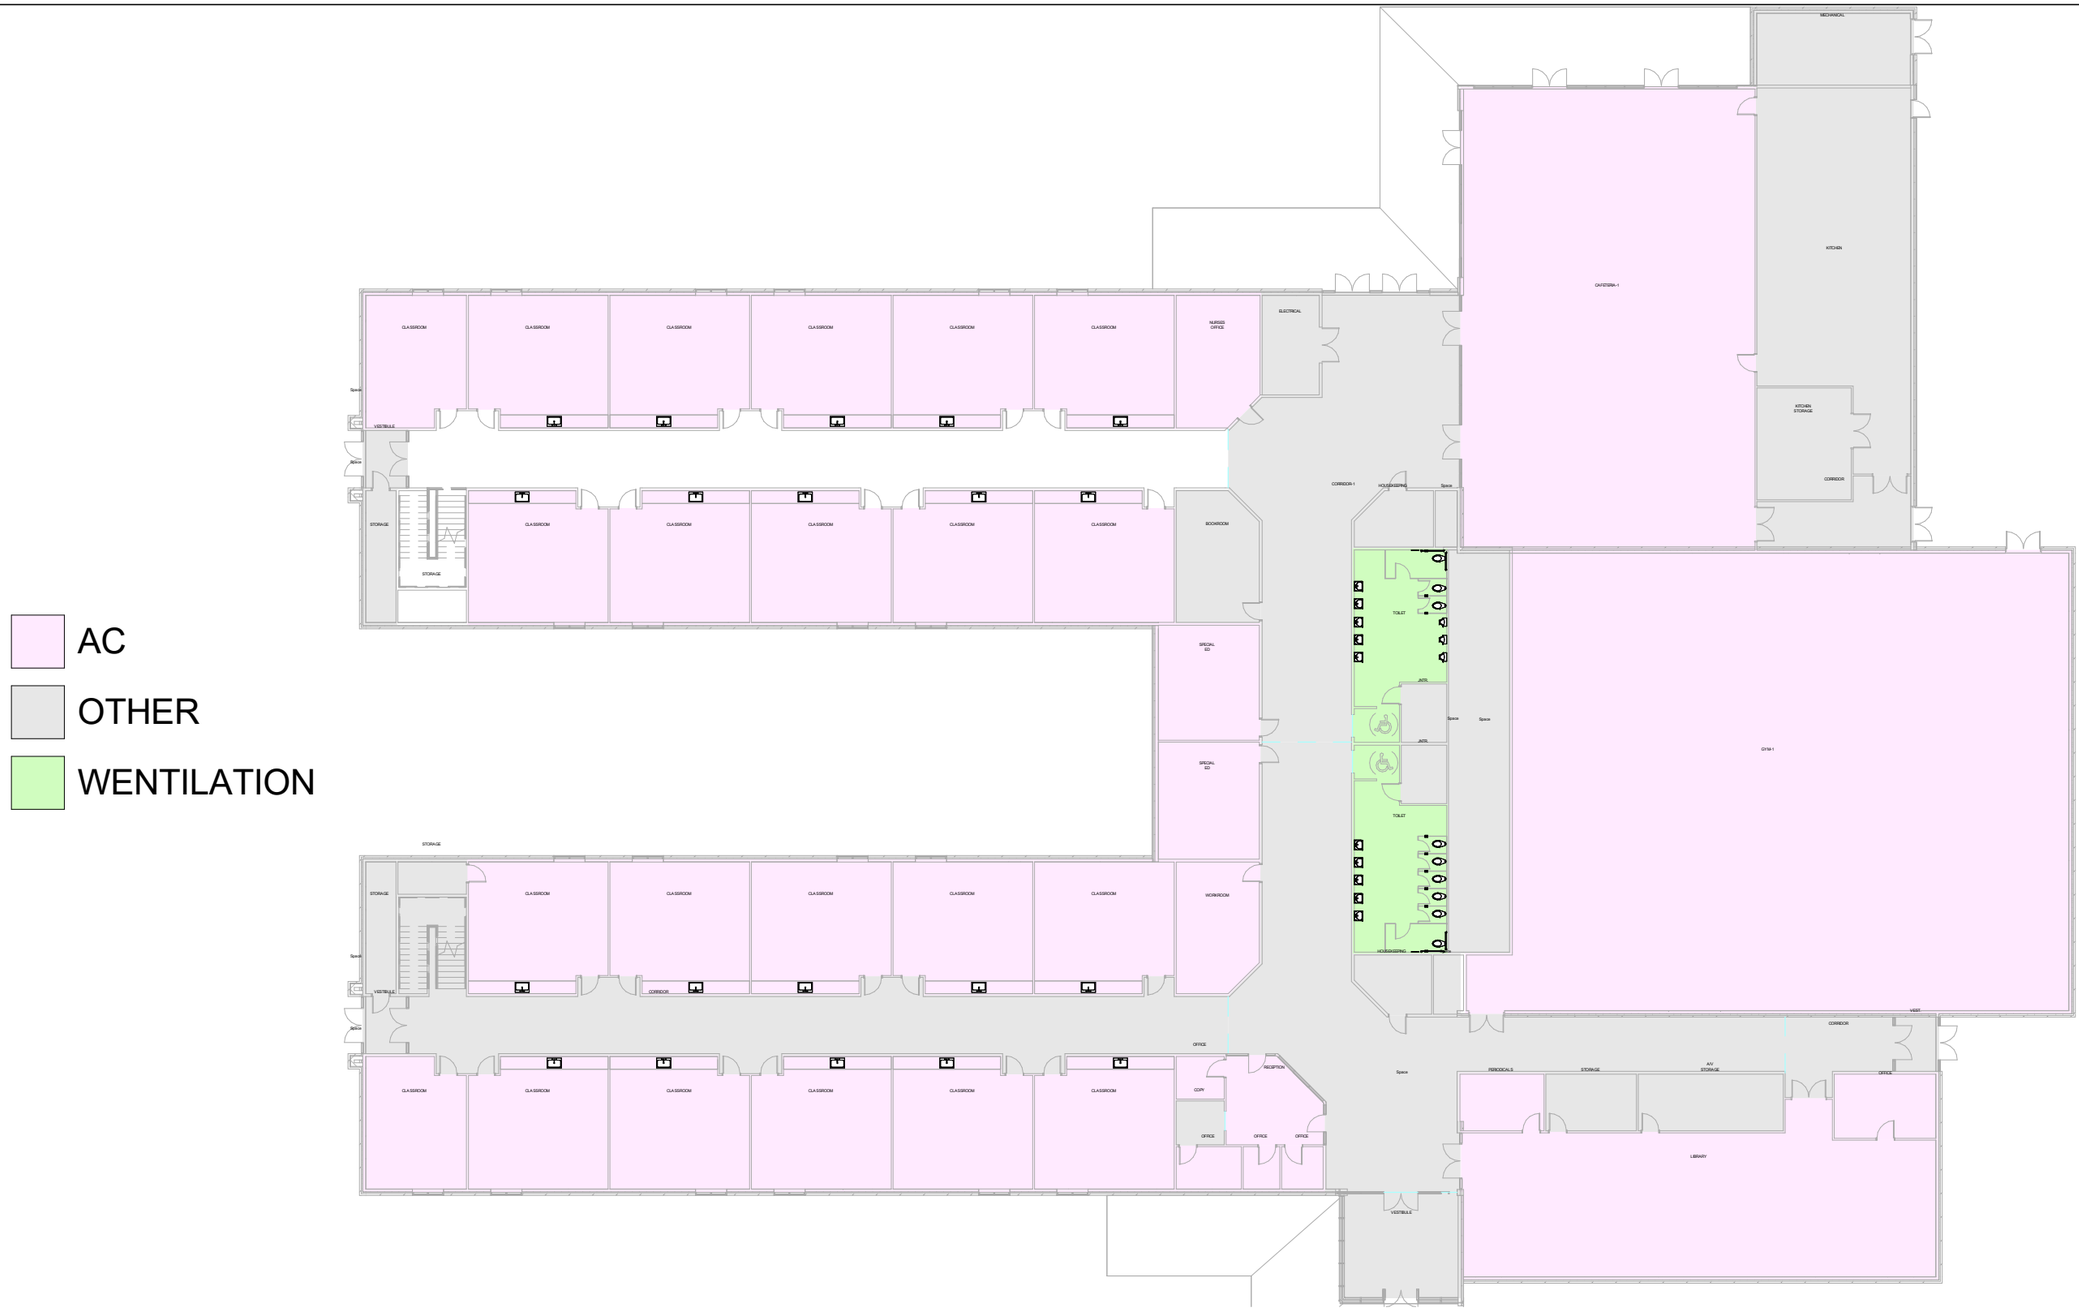


Team Members:

Omar Soliman
Kareem Tarek
Mahmoud Abd Elmawla
Mariem Mohamed
Menna Nasser

OwnerWYZ


Project NameCairo School

01-First Level-Color Coding

Project number	1
Date	October ,2027
Drawn by	Team Members
Checked by	wyz
Scale	1 : 300

A101

10/14/2026 5:42:13 PM

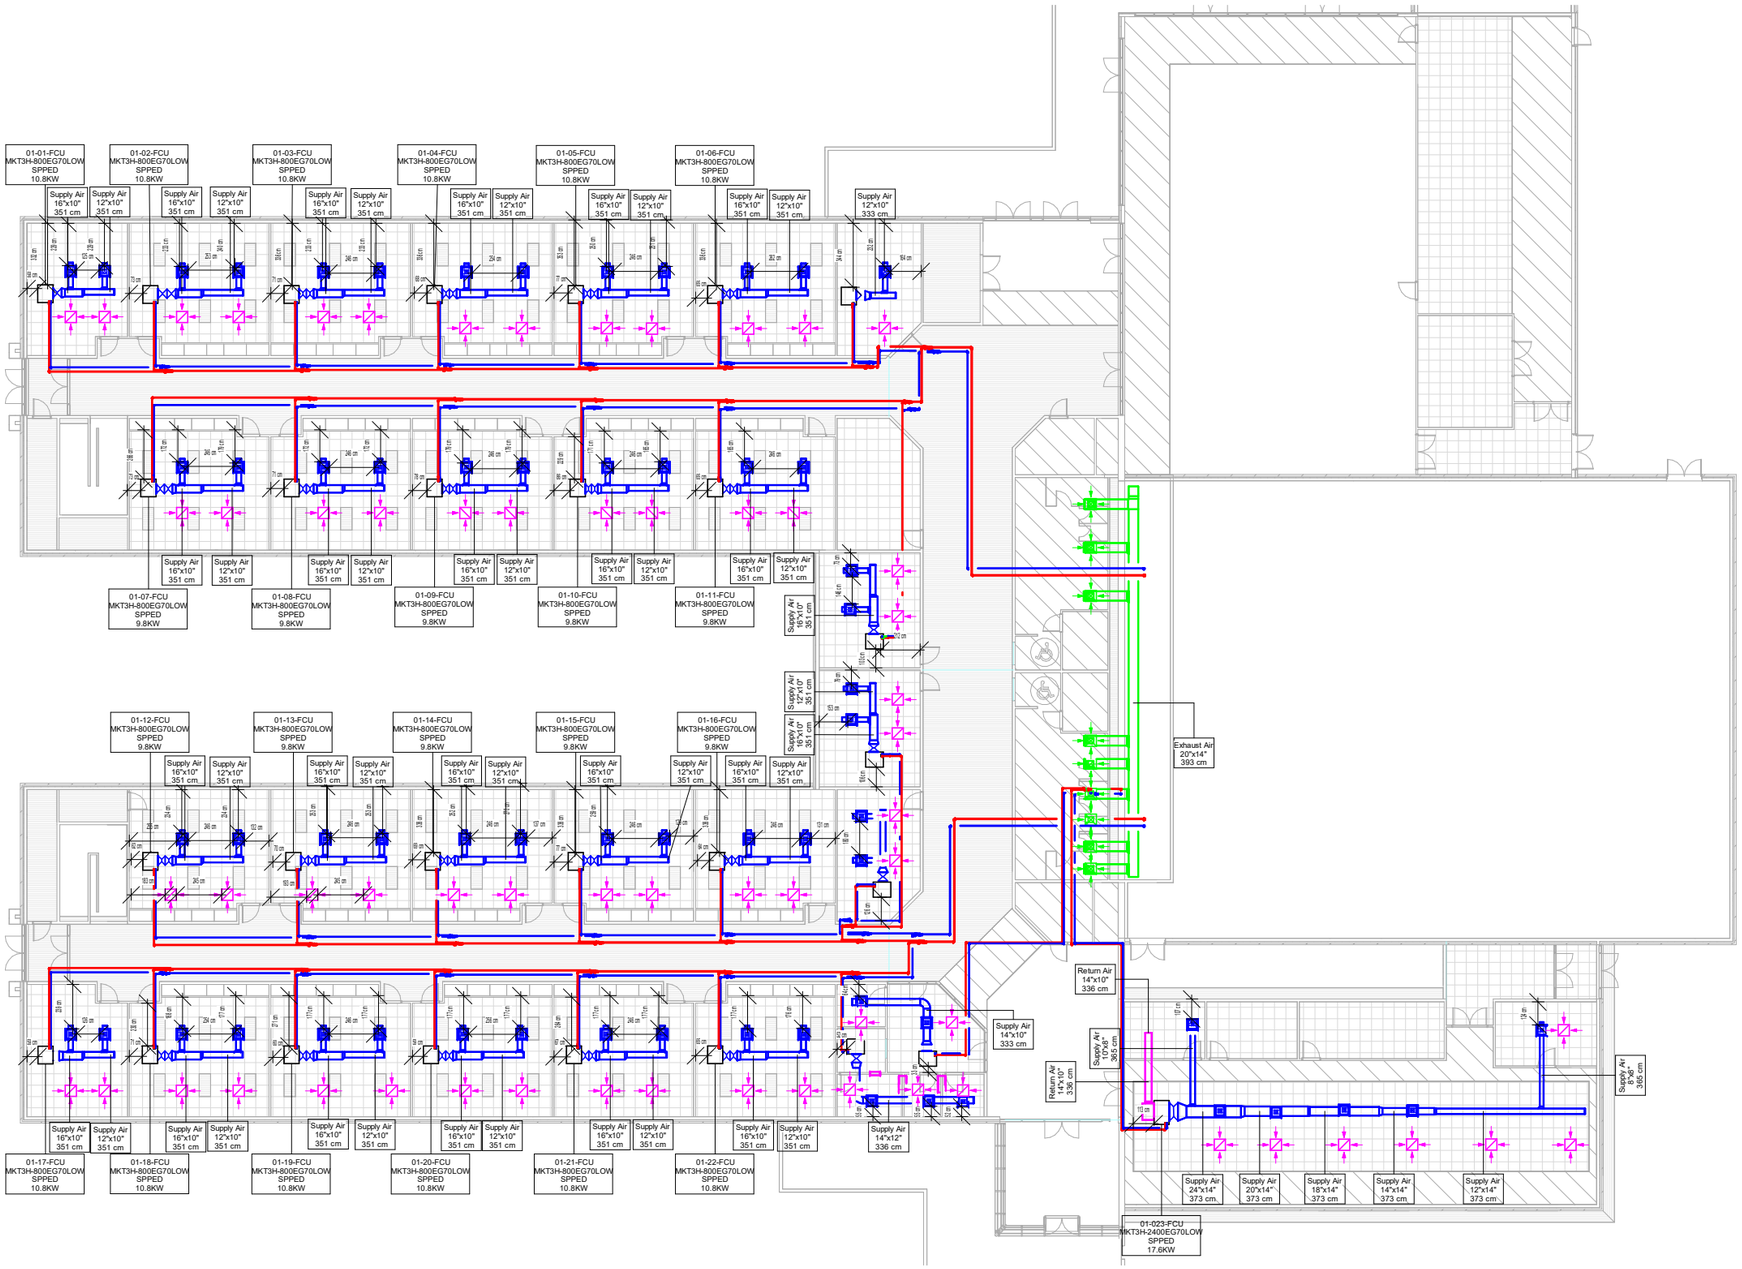

	Supply Difusser
	Return Difusser
	Exhaust Difusser
	Jet Difusser
	Duct
	FCU
	Fan
	Y-Branch
	Roof Drain
	Gate Valve
	Pump

Team Members:

Omar Soliman
Kareem Tarek
Mahmoud Abd Elmawla
Mariem Mohamed
Menna Nasser

Owner :WYZ


Project Name : Cairo School

01-First Level-MECH 1

Project number	1
Date	October,2026
Drawn by	Team member
Checked by	wyz
Scale	As indicated

A102

10/14/2026 2:03:55 PM

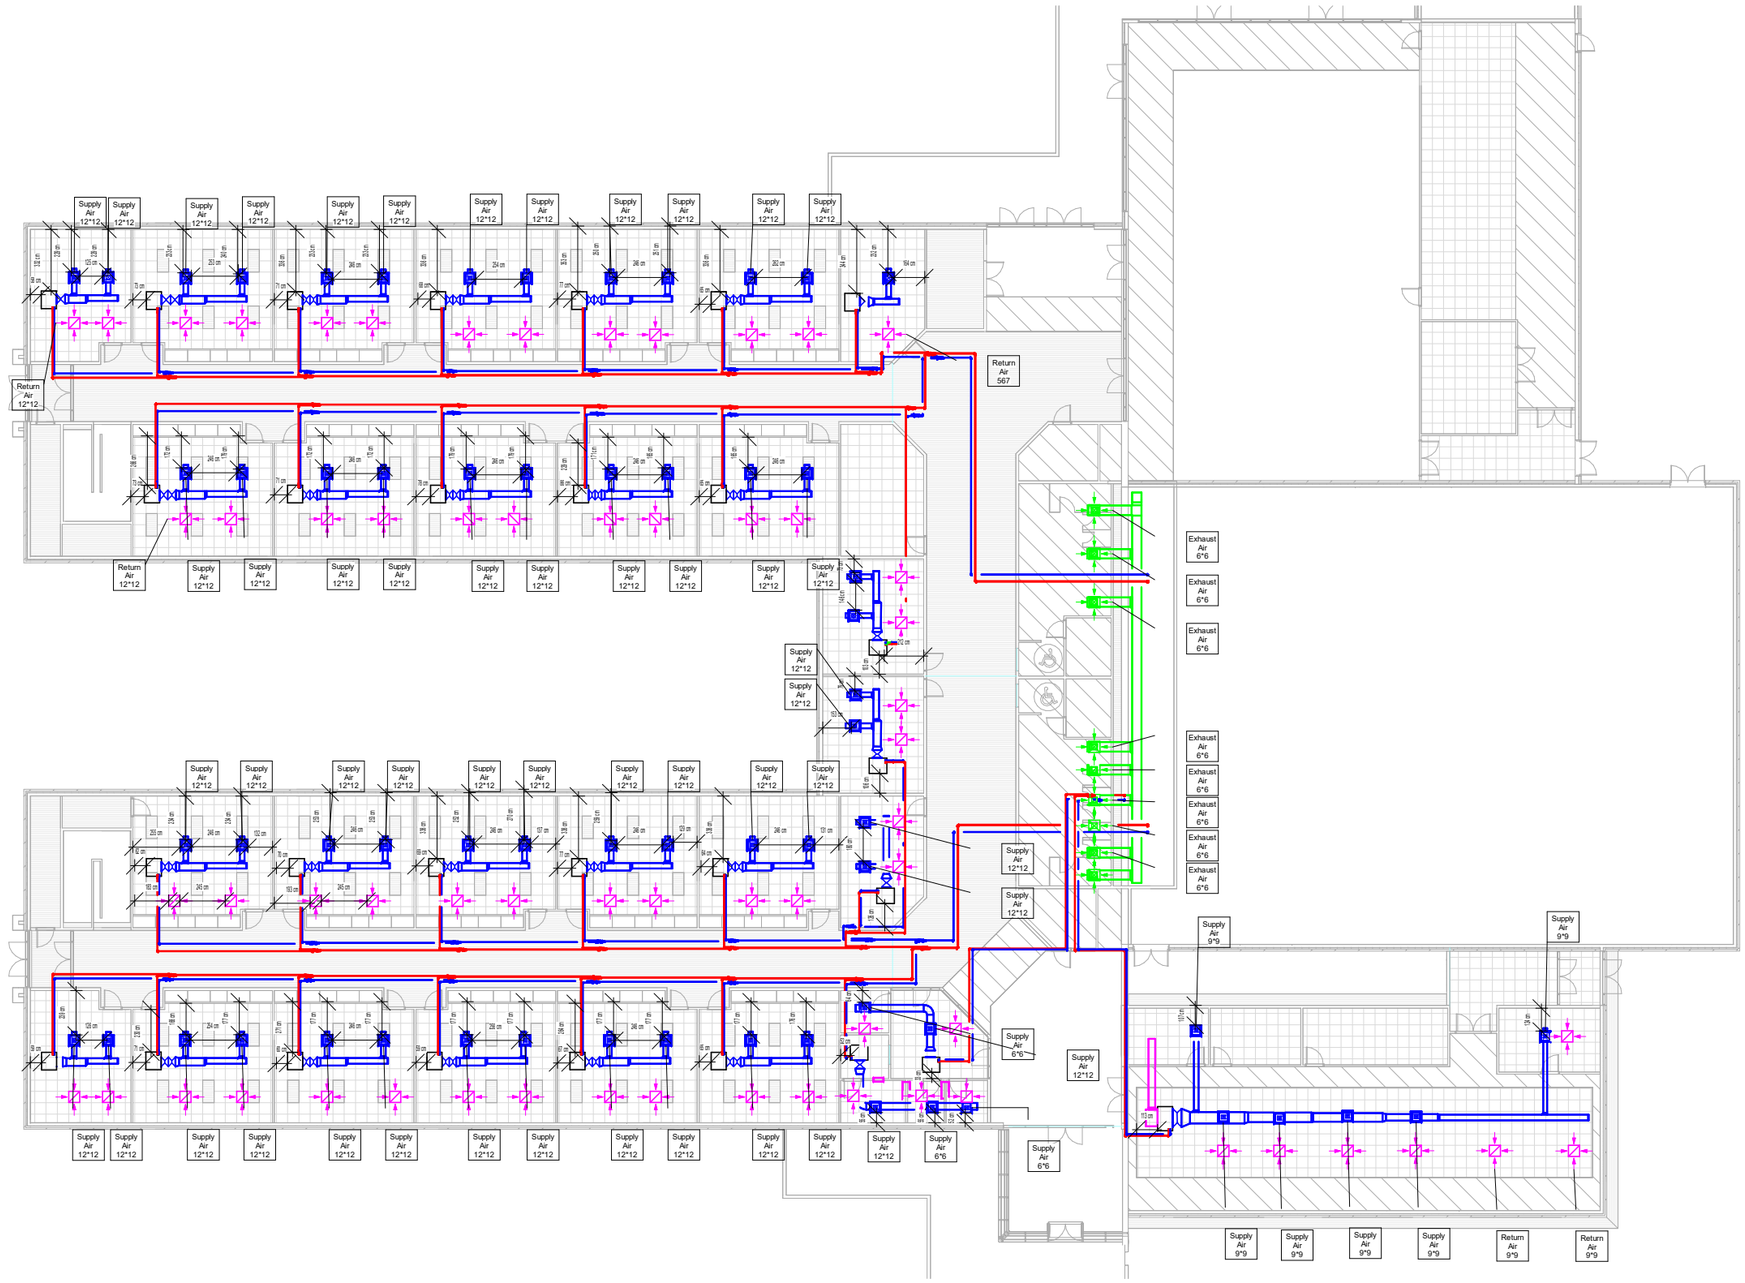

	Supply Difusser
	Return Difusser
	Exhaust Difusser
	Jet Difusser
	Duct
	FCU
	Fan
	Y-Branch
	Roof Drain
	Gate Valve
	Pump

Team Members:

Omar Soliman
Kareem Tarek
Mahmoud Abd Elmawla
Mariem Mohamed
Menna Nasser

Owner :WYZ


Project Name : Cairo School


01-First Level-MECH 2

Project number	1
Date	October,2026
Drawn by	Team member
Checked by	wyz
Scale	As indicated

A103

10/14/2026 2:12:35 PM

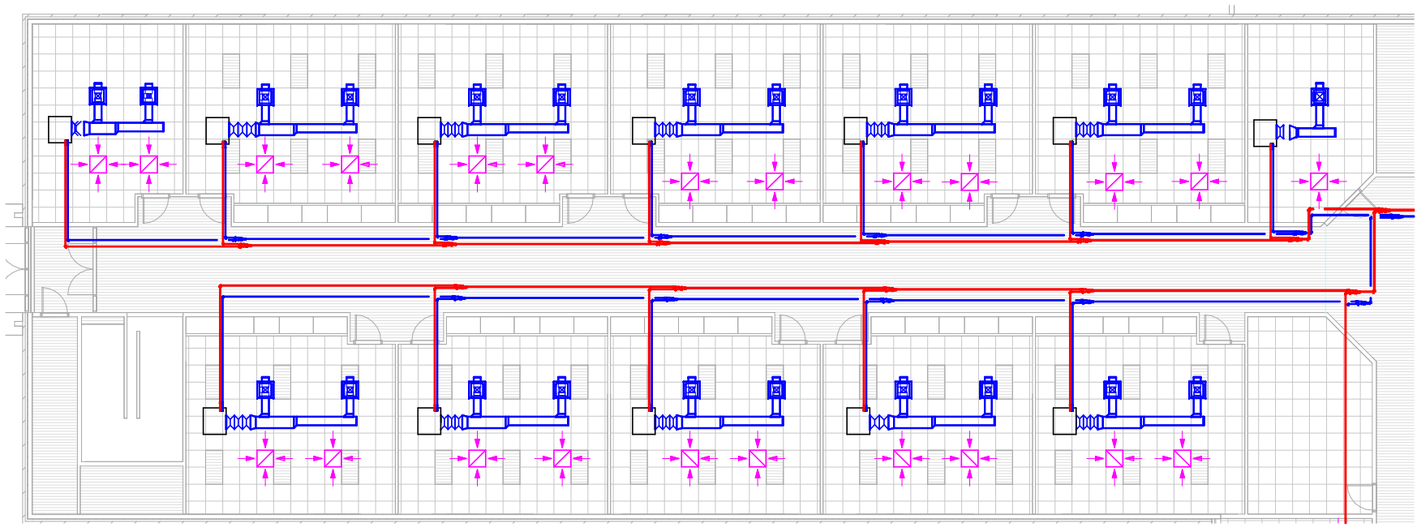

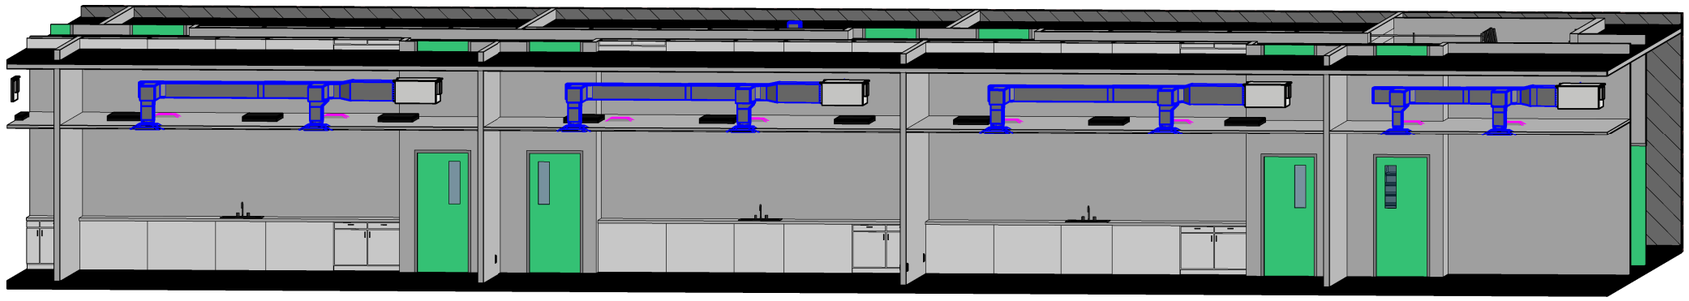

	Supply Difusser
	Return Difusser
	Exhaust Difusser
	Jet Difusser
	Duct
	FCU
	Fan
	Y-Branch
	Roof Drain
	Gate Valve
	Pump

Team Members:

Omar Soliman
Kareem Tarek
Mahmoud Abd Elmawla
Mariem Mohamed
Menna Nasser

Owner :WYZ

Project Name : Cairo School

01-First Level-X-CLIP

Project number	1
Date	October,2026
Drawn by	Team member
Checked by	wyz
Scale	As indicated


A104

10/14/2026 2:29:42 PM

AC

OTHER

WENTILATION

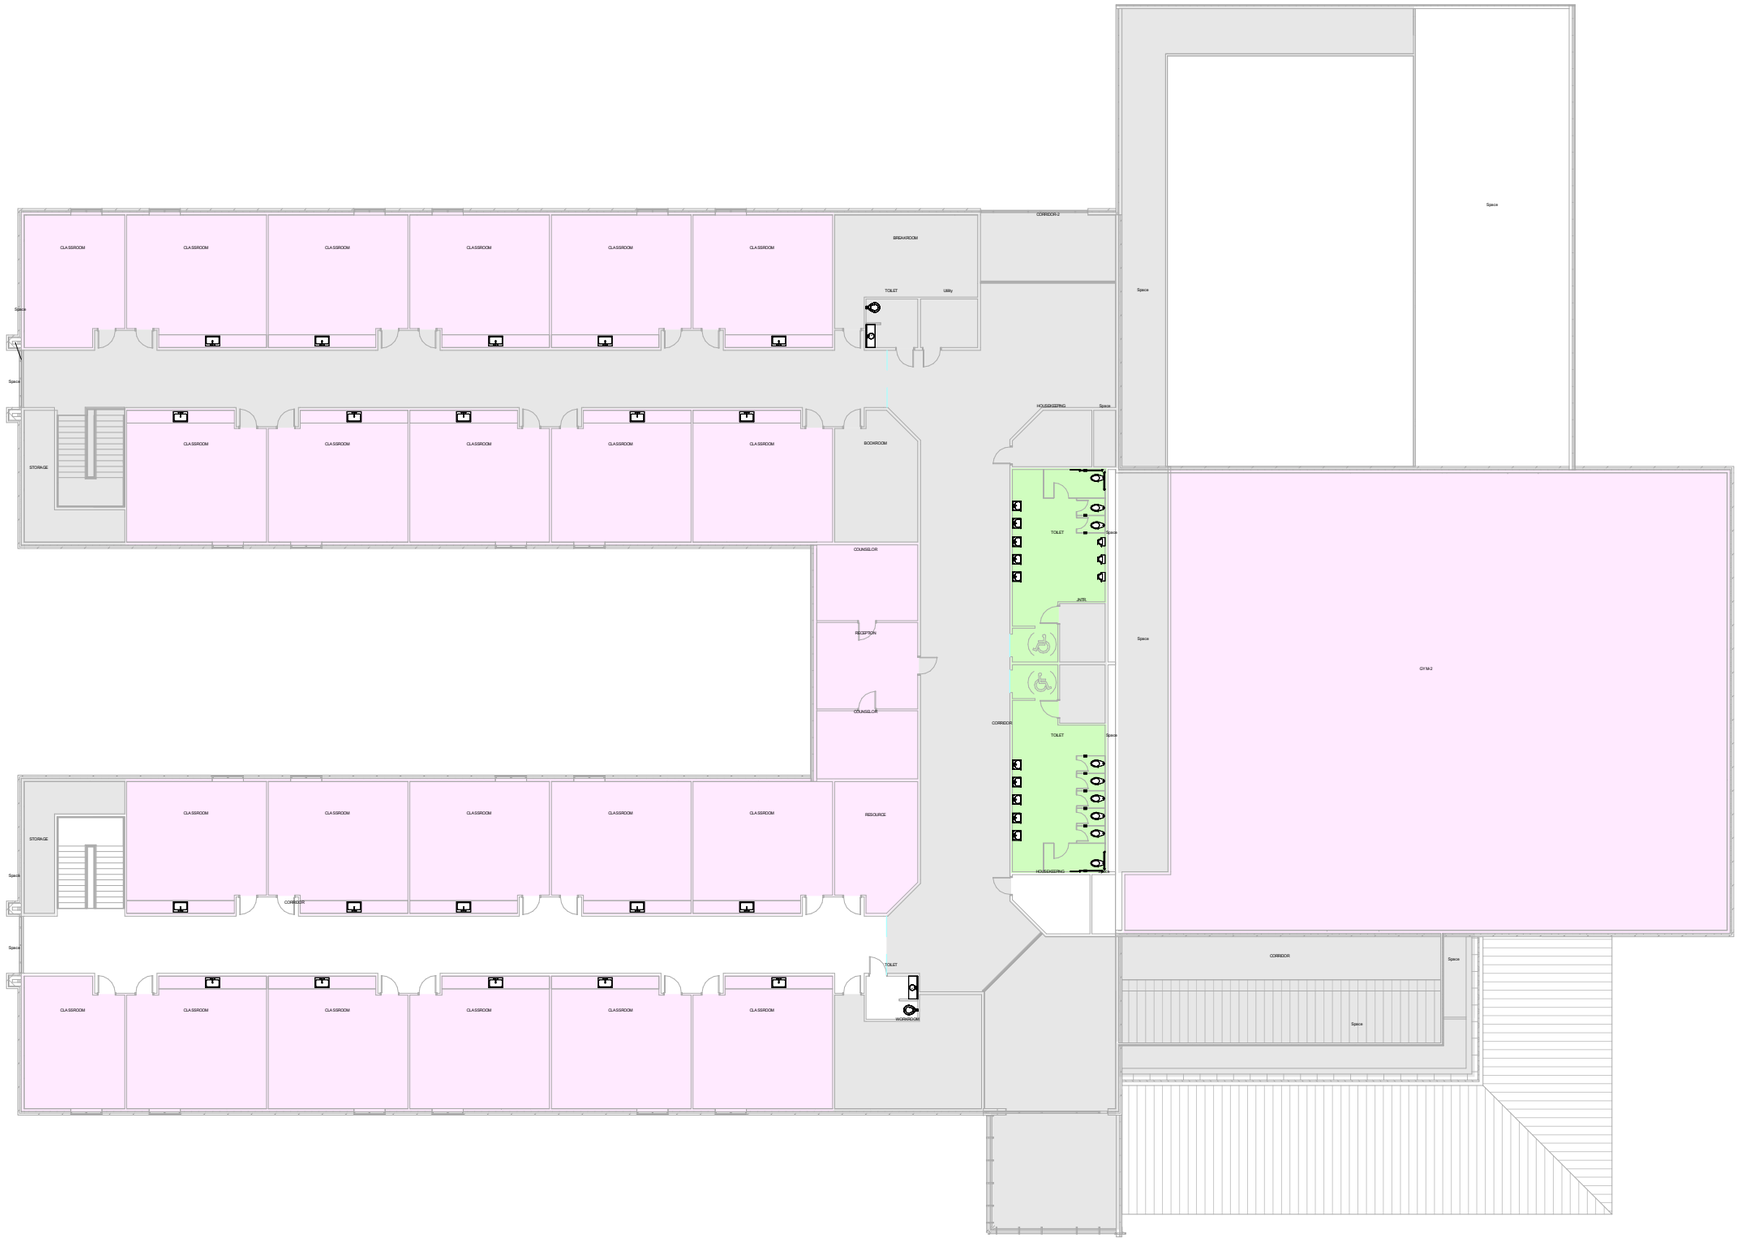

Team Members:

Omar Soliman
Kareem Tarek
Mahmoud Abd Elmawla
Mariem Mohamed
Menna Nasser

OwnerWYZ

Project NameCairo School


02-Secound Level-Color Coding

Project number	1
Date	October ,2027
Drawn by	Team Members
Checked by	wyz

A105

Scale 1 : 300

10/14/2026 5:29:21 PM

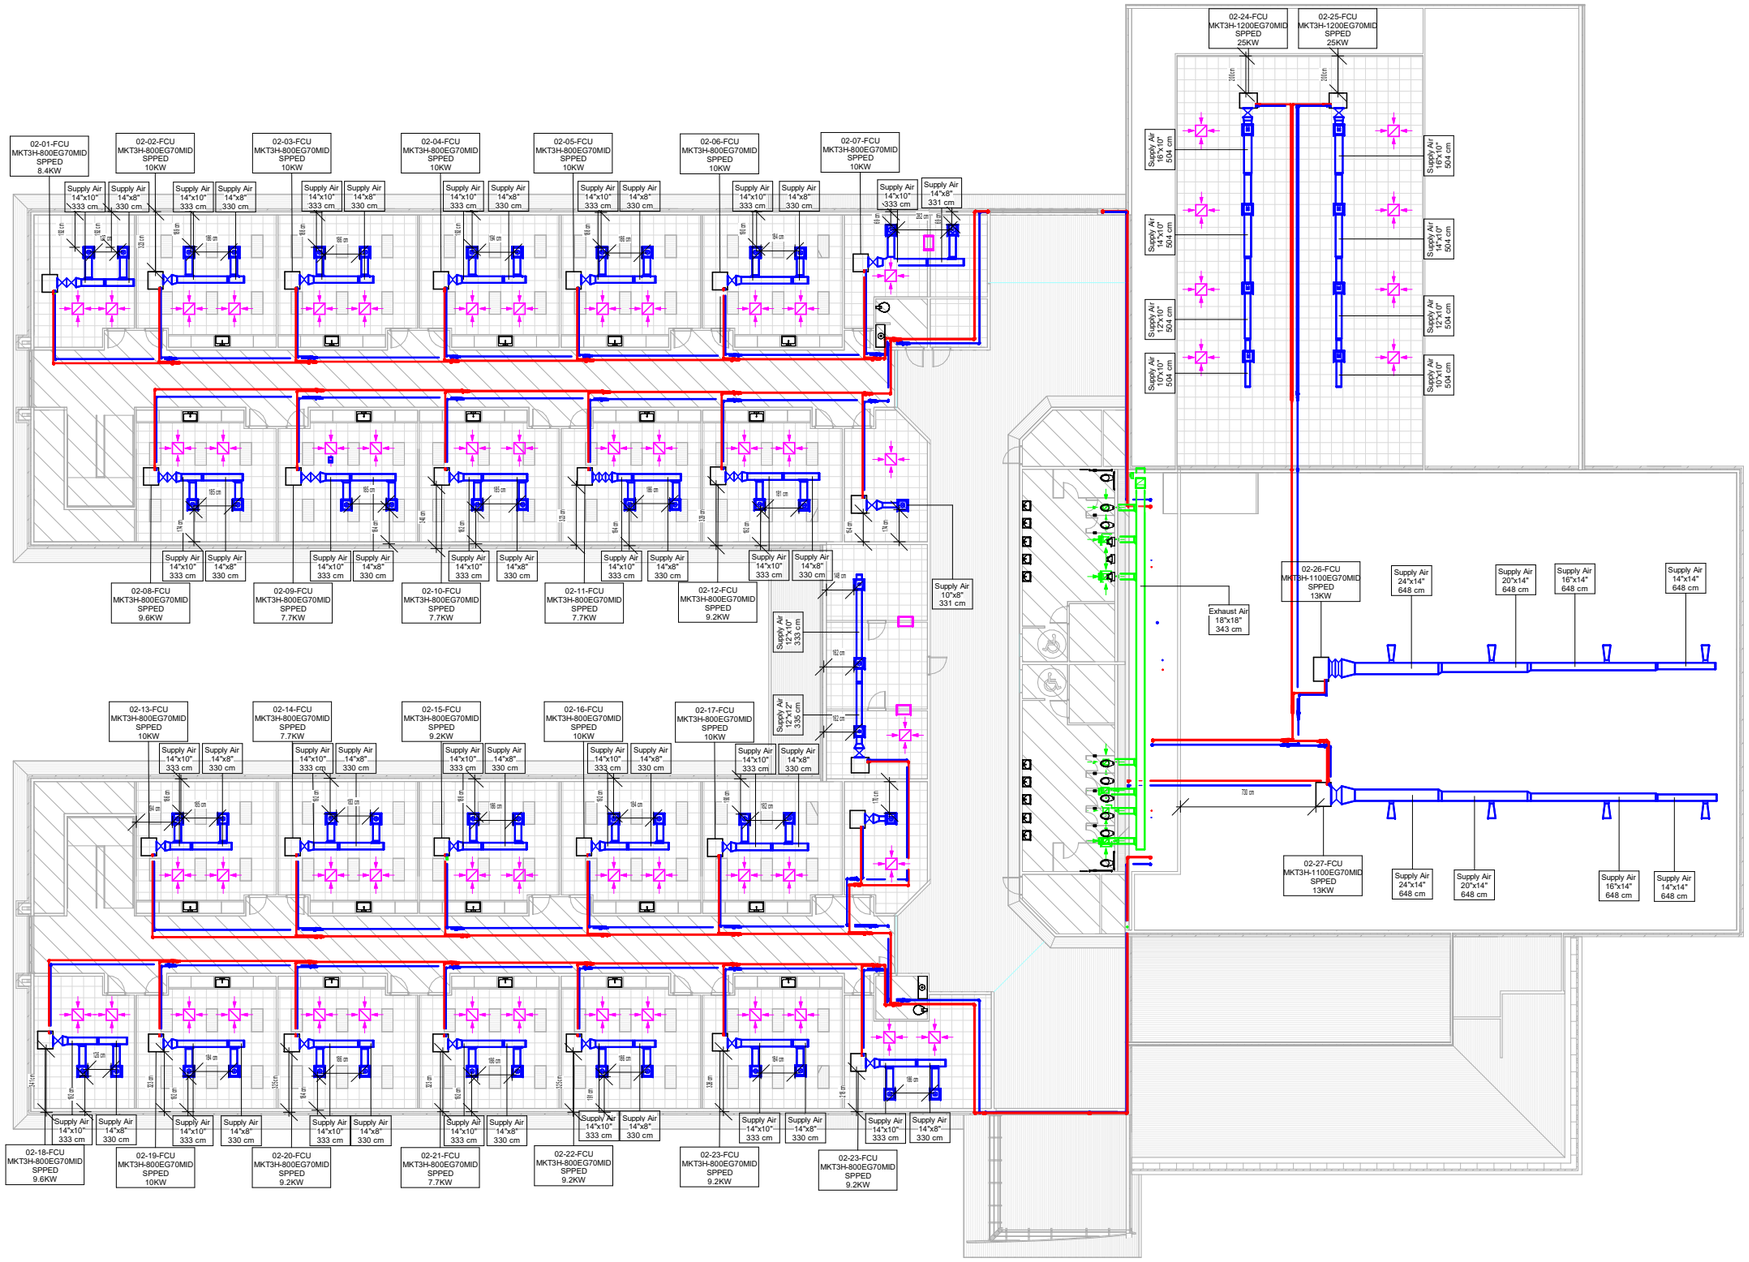

	Supply Difusser
	Return Difusser
	Exhaust Difusser
	Jet Difusser
	Duct
	FCU
	Fan
	Y-Branch
	Roof Drain
	Gate Valve
	Pump

Team Members:

Omar Soliman
Kareem Tarek
Mahmoud Abd Elmawla
Mariem Mohamed
Menna Nasser

Owner :WYZ


Project Name : Cairo School

02-Secound Level-Mech1

Project number	1
Date	October,2026
Drawn by	Team member
Checked by	wyz
Scale	As indicated

A106

10/14/2026 3:28:50 PM

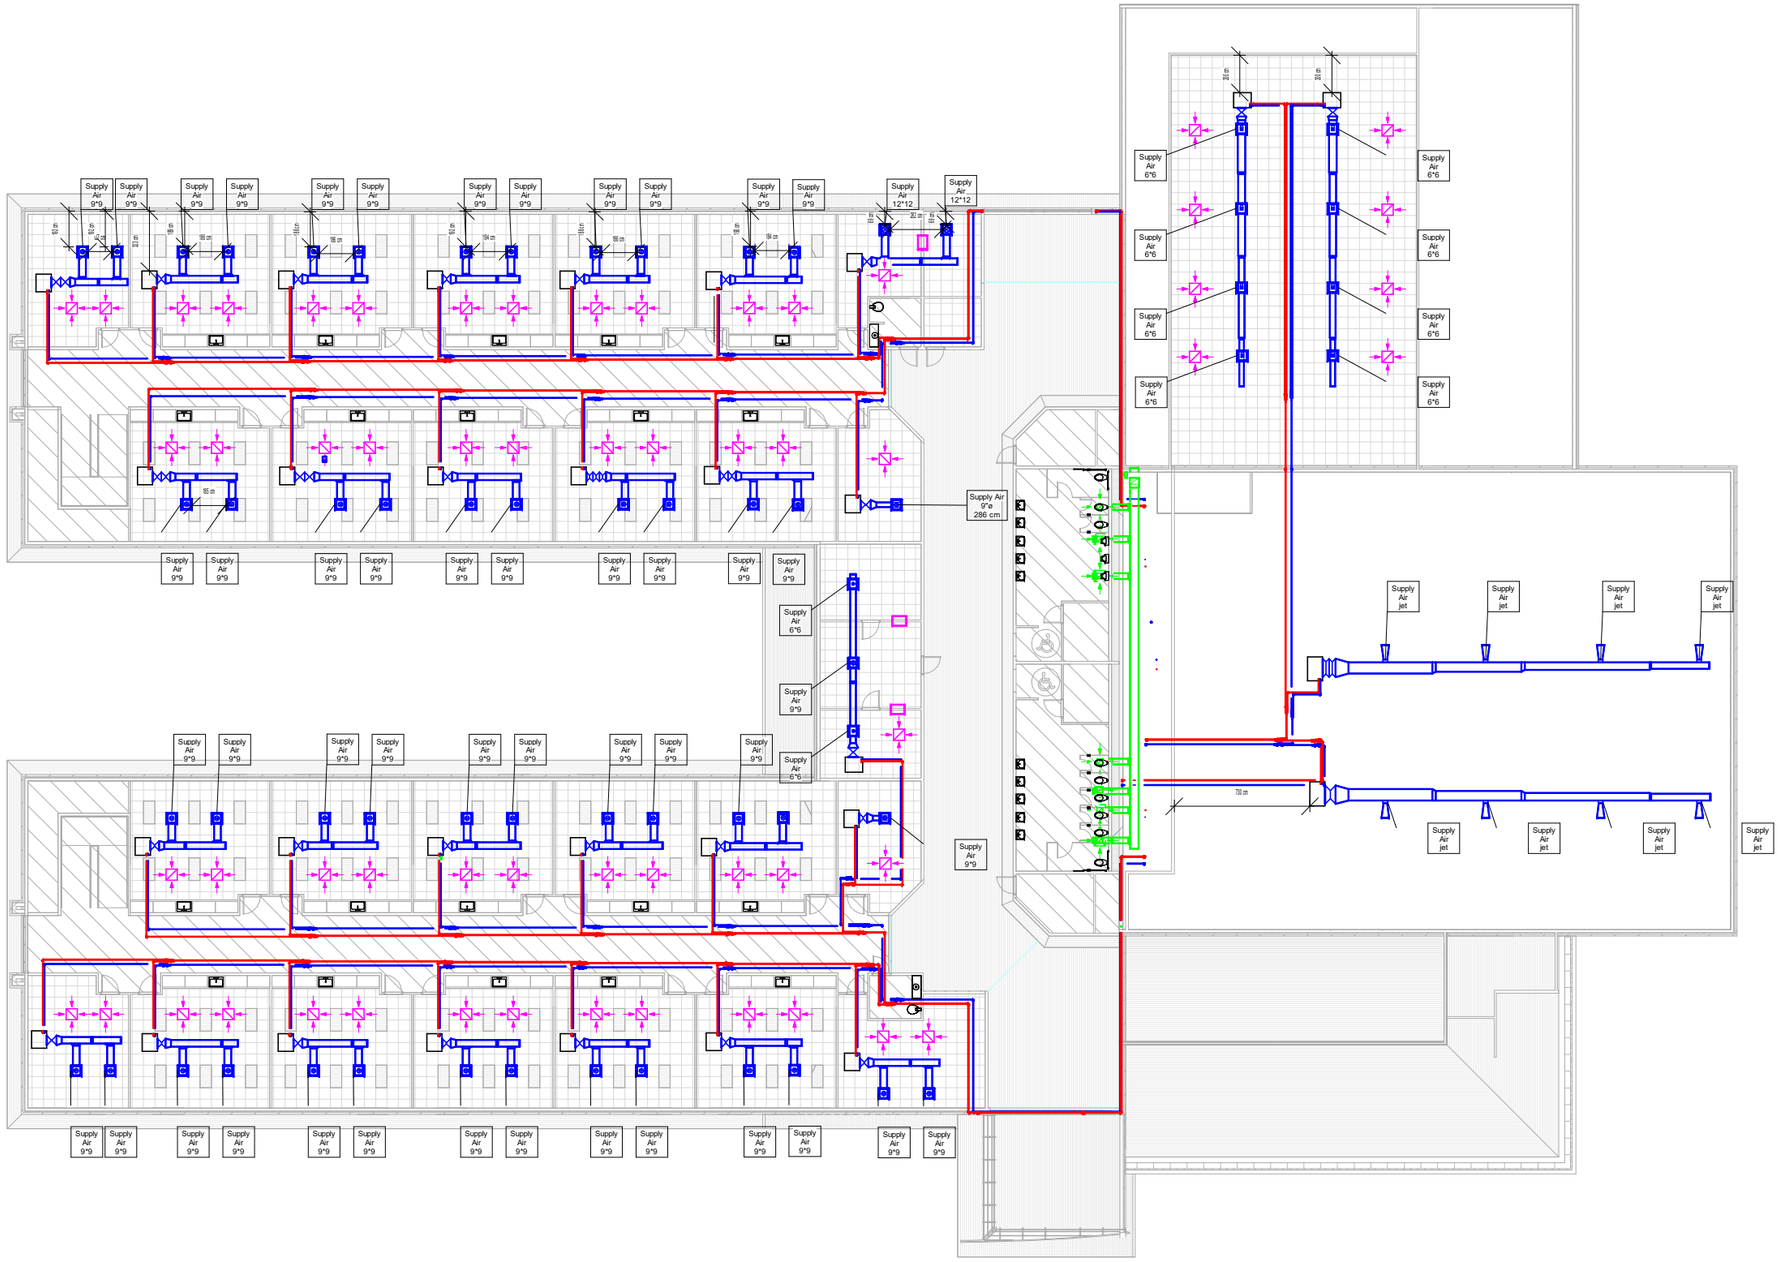

	Supply Difusser
	Return Difusser
	Exhaust Difusser
	Jet Difusser
	Duct
	FCU
	Fan
	Y-Branch
	Roof Drain
	Gate Valve
	Pump

Team Members:

Omar Soliman
Kareem Tarek
Mahmoud Abd Elmawla
Mariem Mohamed
Menna Nasser

Owner :WYZ


Project Name : Cairo School


02-Secound Level-Mech2

Project number	1
Date	October,2026
Drawn by	Team member
Checked by	wyz
Scale	As indicated

A107

10/14/2026 3:33:16 PM

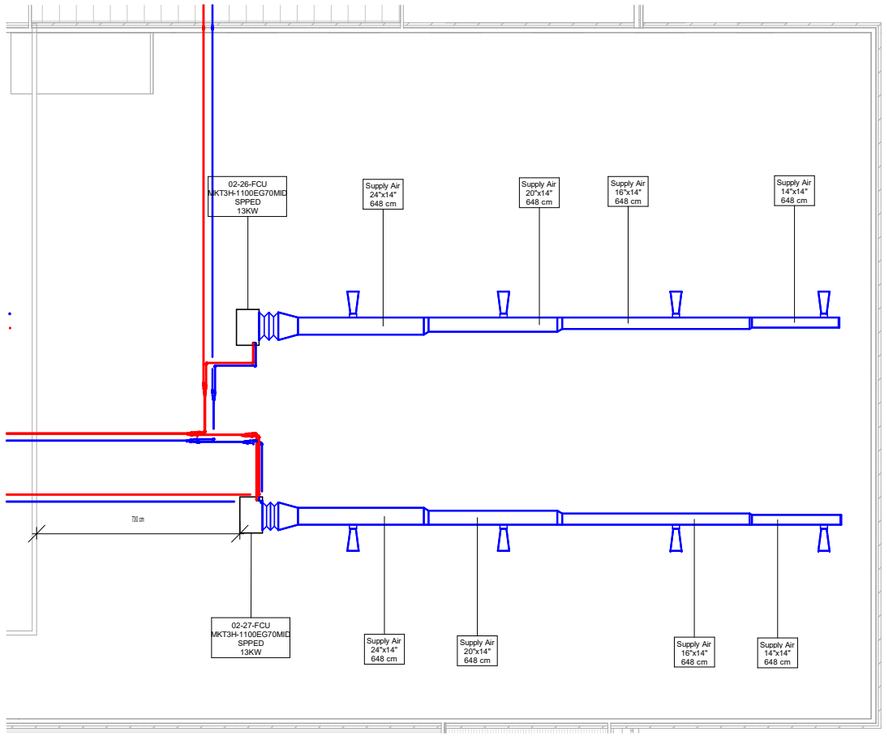

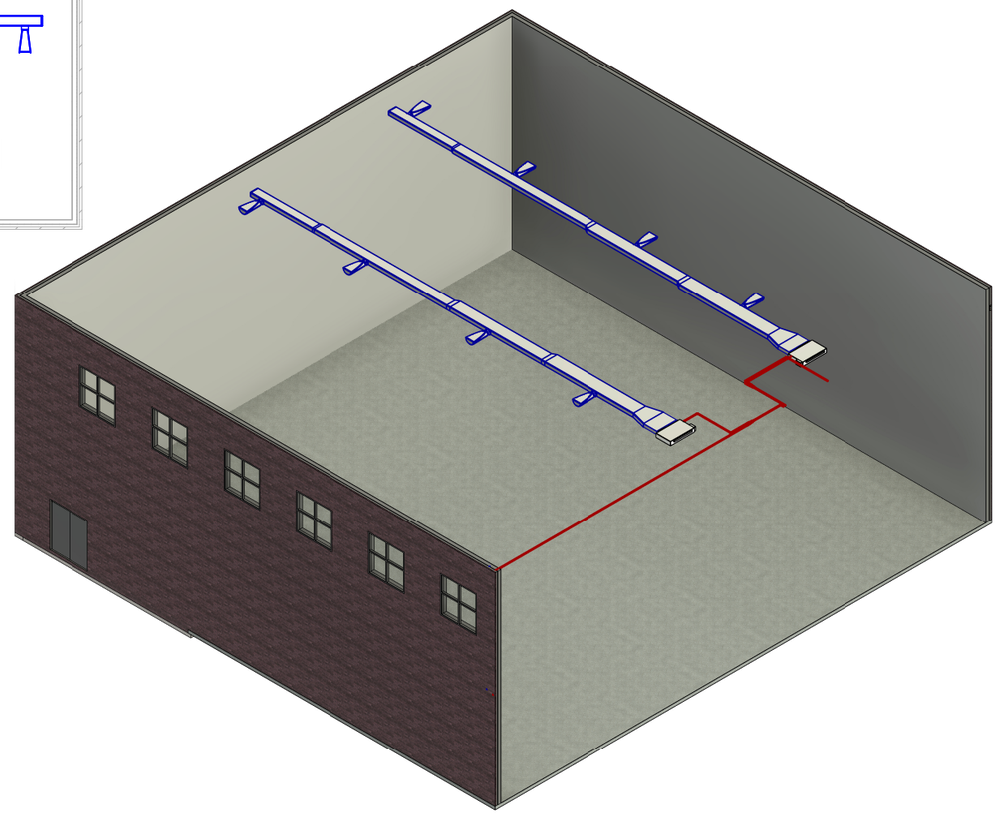

	Supply Difusser
	Return Difusser
	Exhaust Difusser
	Jet Difusser
	Duct
	FCU
	Fan
	Y-Branch
	Roof Drain
	Gate Valve
	Pump

Team Members:

Omar Soliman
Kareem Tarek
Mahmoud Abd Elmawla
Mariem Mohamed
Menna Nasser

Owner :WYZ


Project Name : Cairo School


02-Secound Level-X-CLIP

Project number	1
Date	October,2026
Drawn by	Team member
Checked by	wyz
Scale	As indicated

A108

10/14/2026 3:49:06 PM

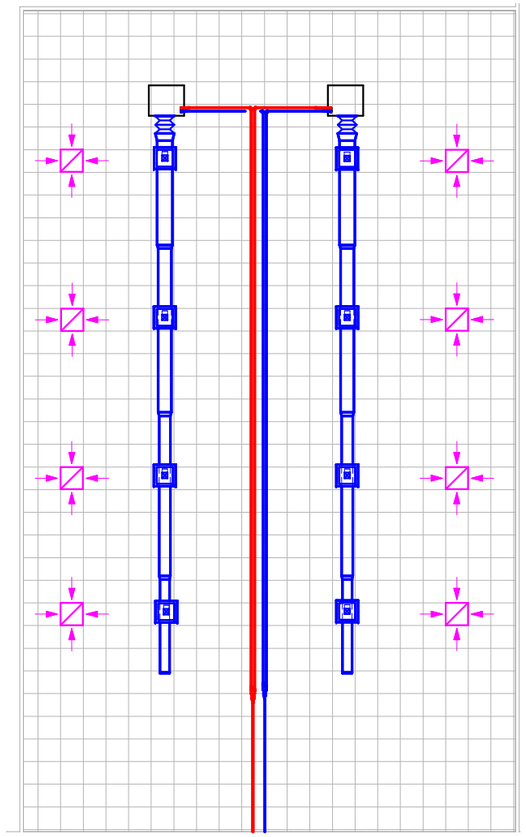

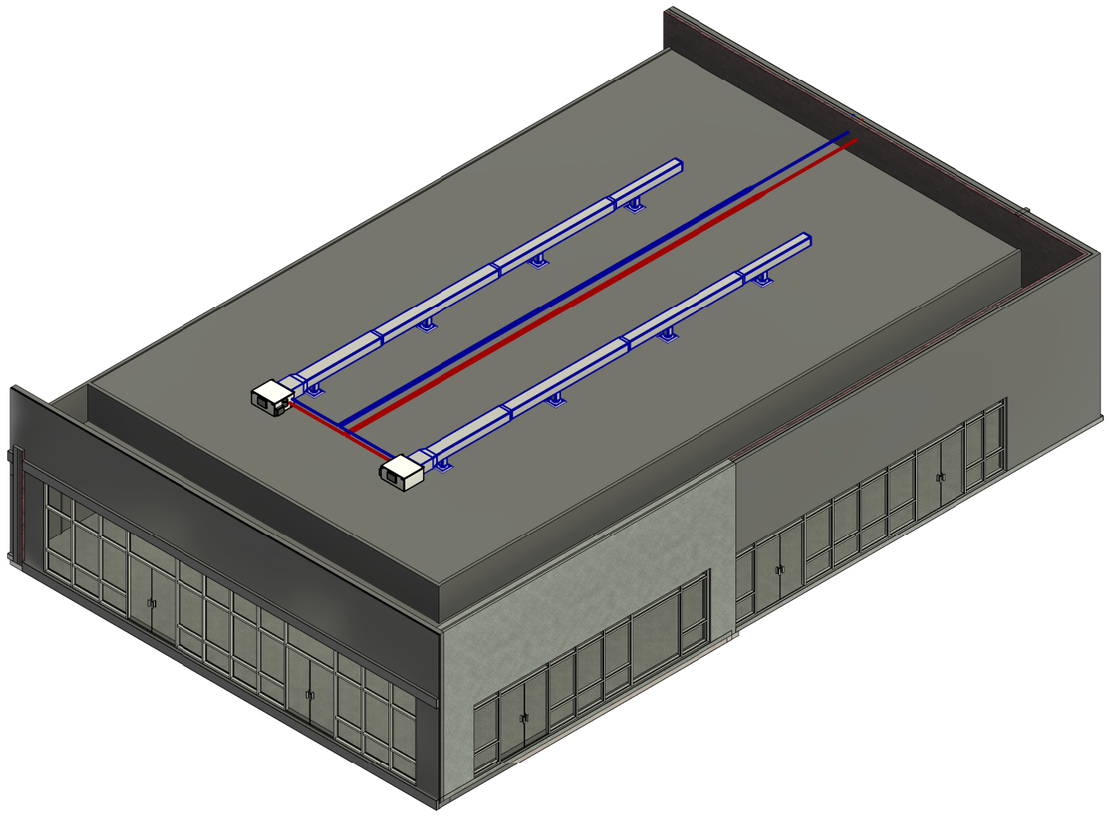

	Supply Difusser
	Return Difusser
	Exhaust Difusser
	Jet Difusser
	Duct
	FCU
	Fan
	Y-Branch
	Roof Drain
	Gate Valve
	Pump

Team Members:

Omar Soliman
Kareem Tarek
Mahmoud Abd Elmawla
Mariem Mohamed
Menna Nasser

Owner :WYZ


Project Name : Cairo School

02-Secound Level-X-CLIP

Project number	1
Date	October,2026
Drawn by	Team member
Checked by	wyz
Scale	As indicated

A109

10/14/2026 4:01:53 PM

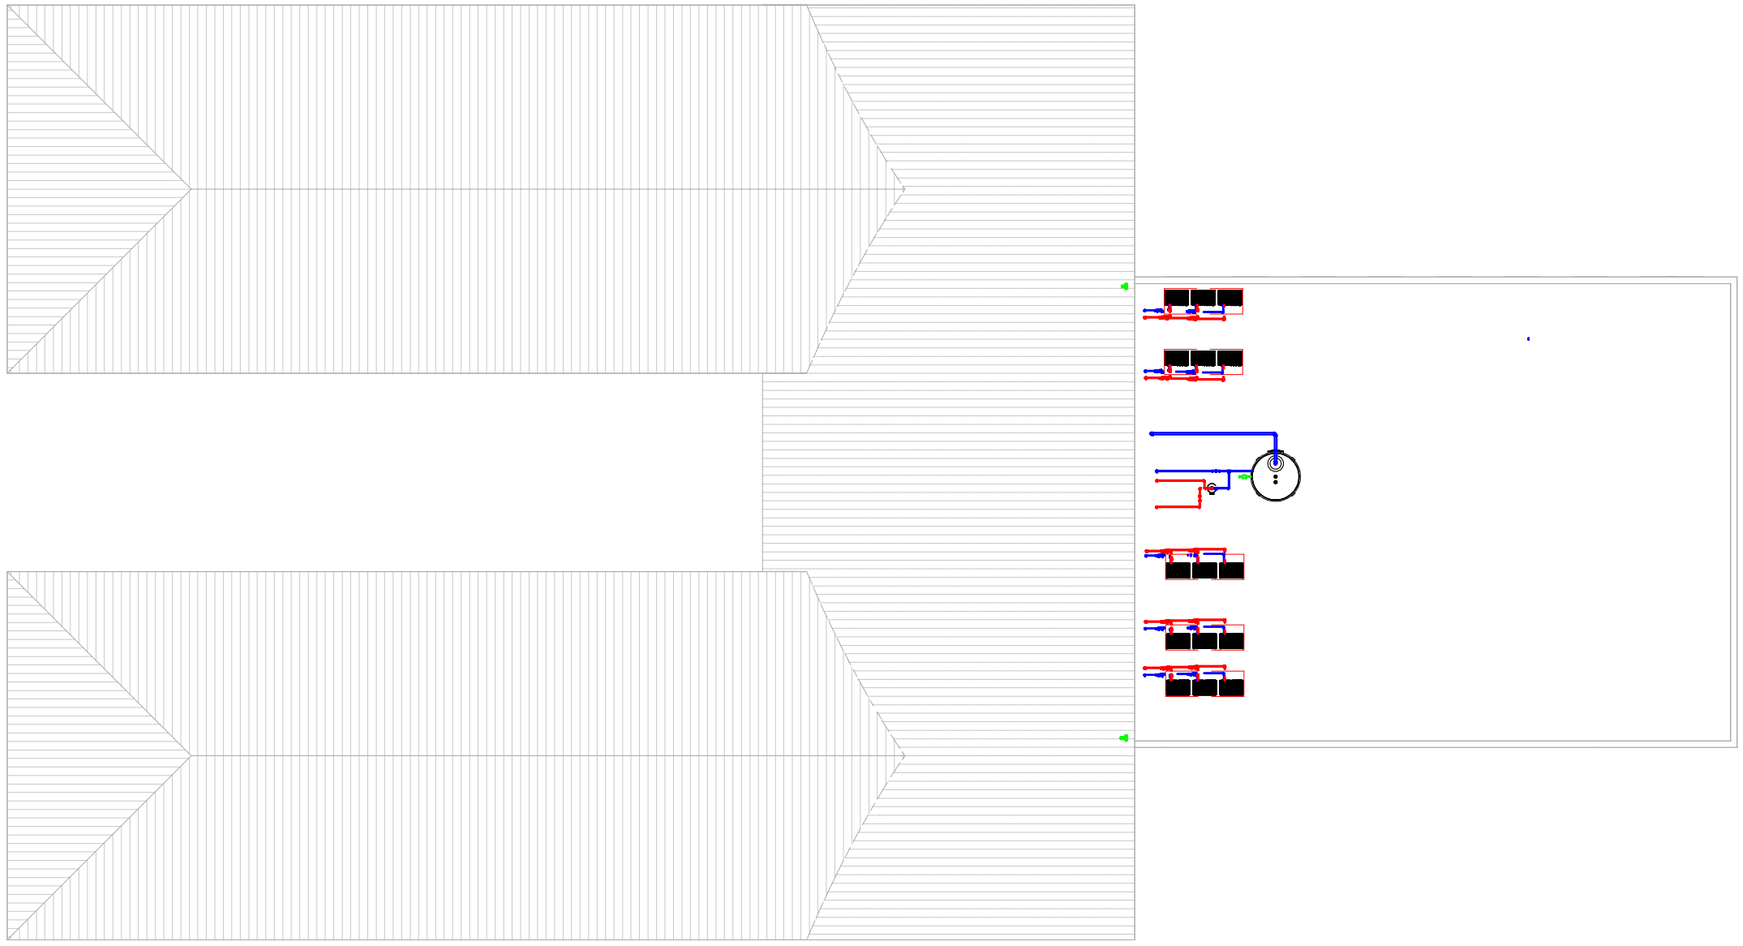

	Supply Difusser
	Return Difusser
	Exhaust Difusser
	Jet Difusser
	Duct
	FCU
	Fan
	Y-Branch
	Roof Drain
	Gate Valve
	Pump

Team Members:

Omar Soliman
Kareem Tarek
Mahmoud Abd Elmawla
Mariem Mohamed
Menna Nasser

Owner :WYZ


Project Name : Cairo School

03-POOF

Project number	1
Date	October,2026
Drawn by	Team member
Checked by	wyz
Scale	As indicated

A110

10/14/2026 4:37:40 PM

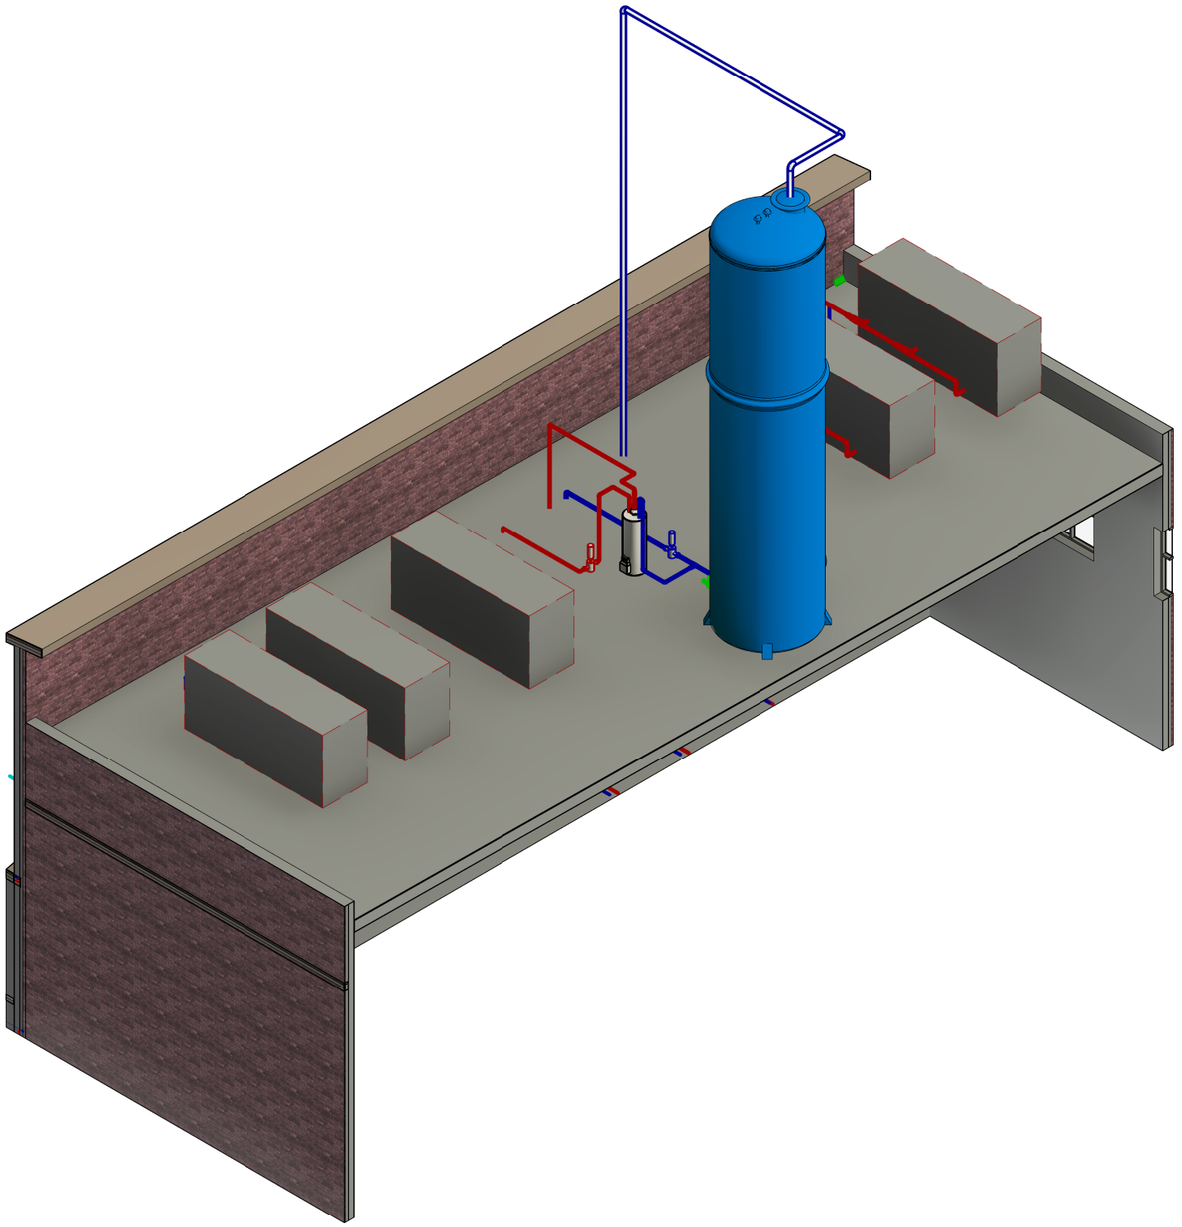

	Supply Difusser
	Return Difusser
	Exhaust Difusser
	Jet Difusser
	Duct
	FCU
	Fan
	Y-Branch
	Roof Drain
	Gate Valve
	Pump

Team Members:

Omar Soliman
Kareem Tarek
Mahmoud Abd Elmawla
Mariem Mohamed
Menna Nasser

Owner :WYZ

Project Name : Cairo School

03-POOF-3D

Project number	1
Date	October,2026
Drawn by	Team member
Checked by	wyz
Scale	1 : 50

A111

10/14/2026 4:33:51 PM