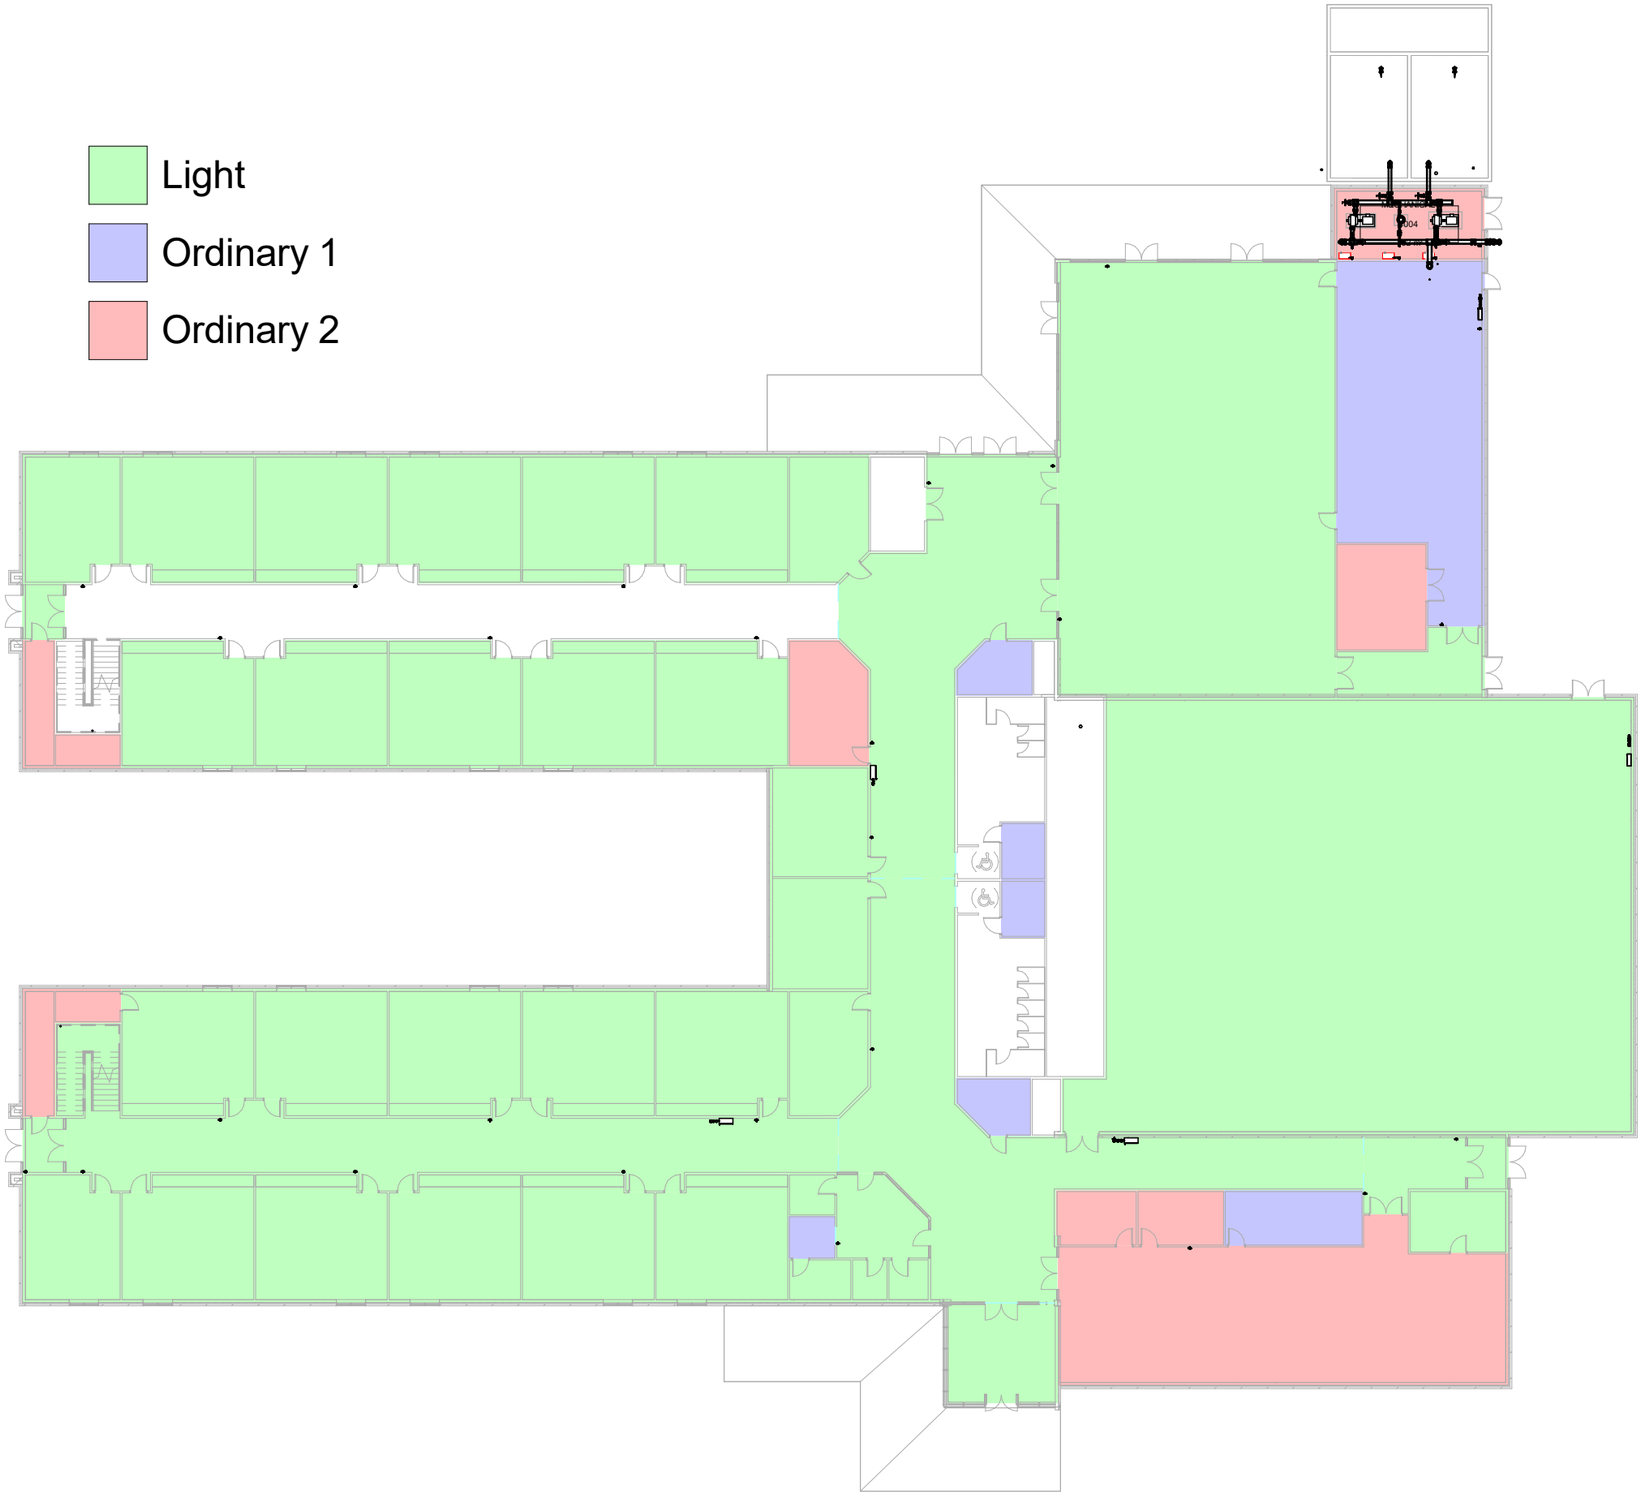


Team Members:

Omar Soliman
Kareem Tarek
Mahmoud Abdelmawla
Mariem Mohamed
Menna Nasser

Owner : WYZ


Project Name : Cairo School

COLOR CODING 1

Project number	1
Date	16-oct-2026
Drawn by	OK&3M
Checked by	WYZ
Scale	1 : 350

00

10/15/2026 8:58:43 PM

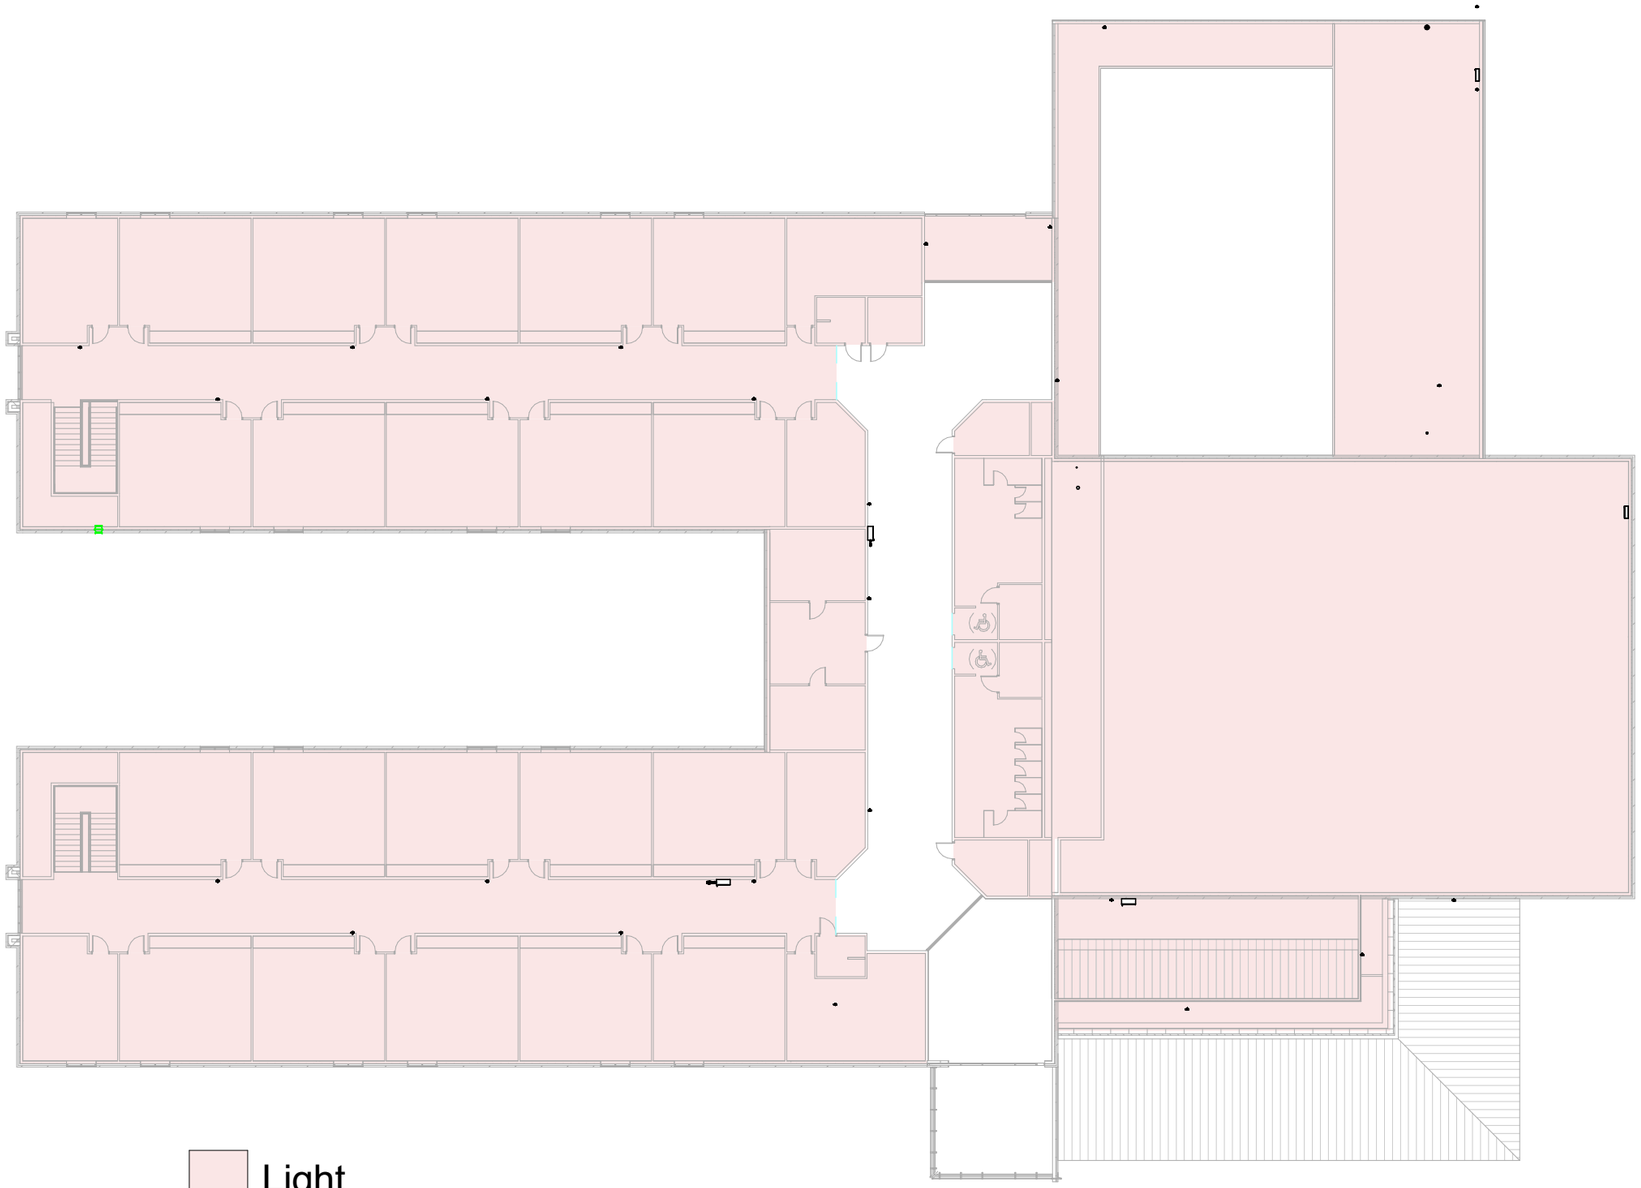

Light

Team Members:

Omar Soliman
Kareem Tarek
Mahmoud Abdelmawla
Mariem Mohamed
Menna Nasser


Owner : WYZ

Project Name : Cairo School

COLOR CODING 2

Project number	1	01	
Date	16-oct-2026		
Drawn by	OK&3M		
Checked by	WYZ	Scale	1 : 350

10/15/2026 9:23:33 PM

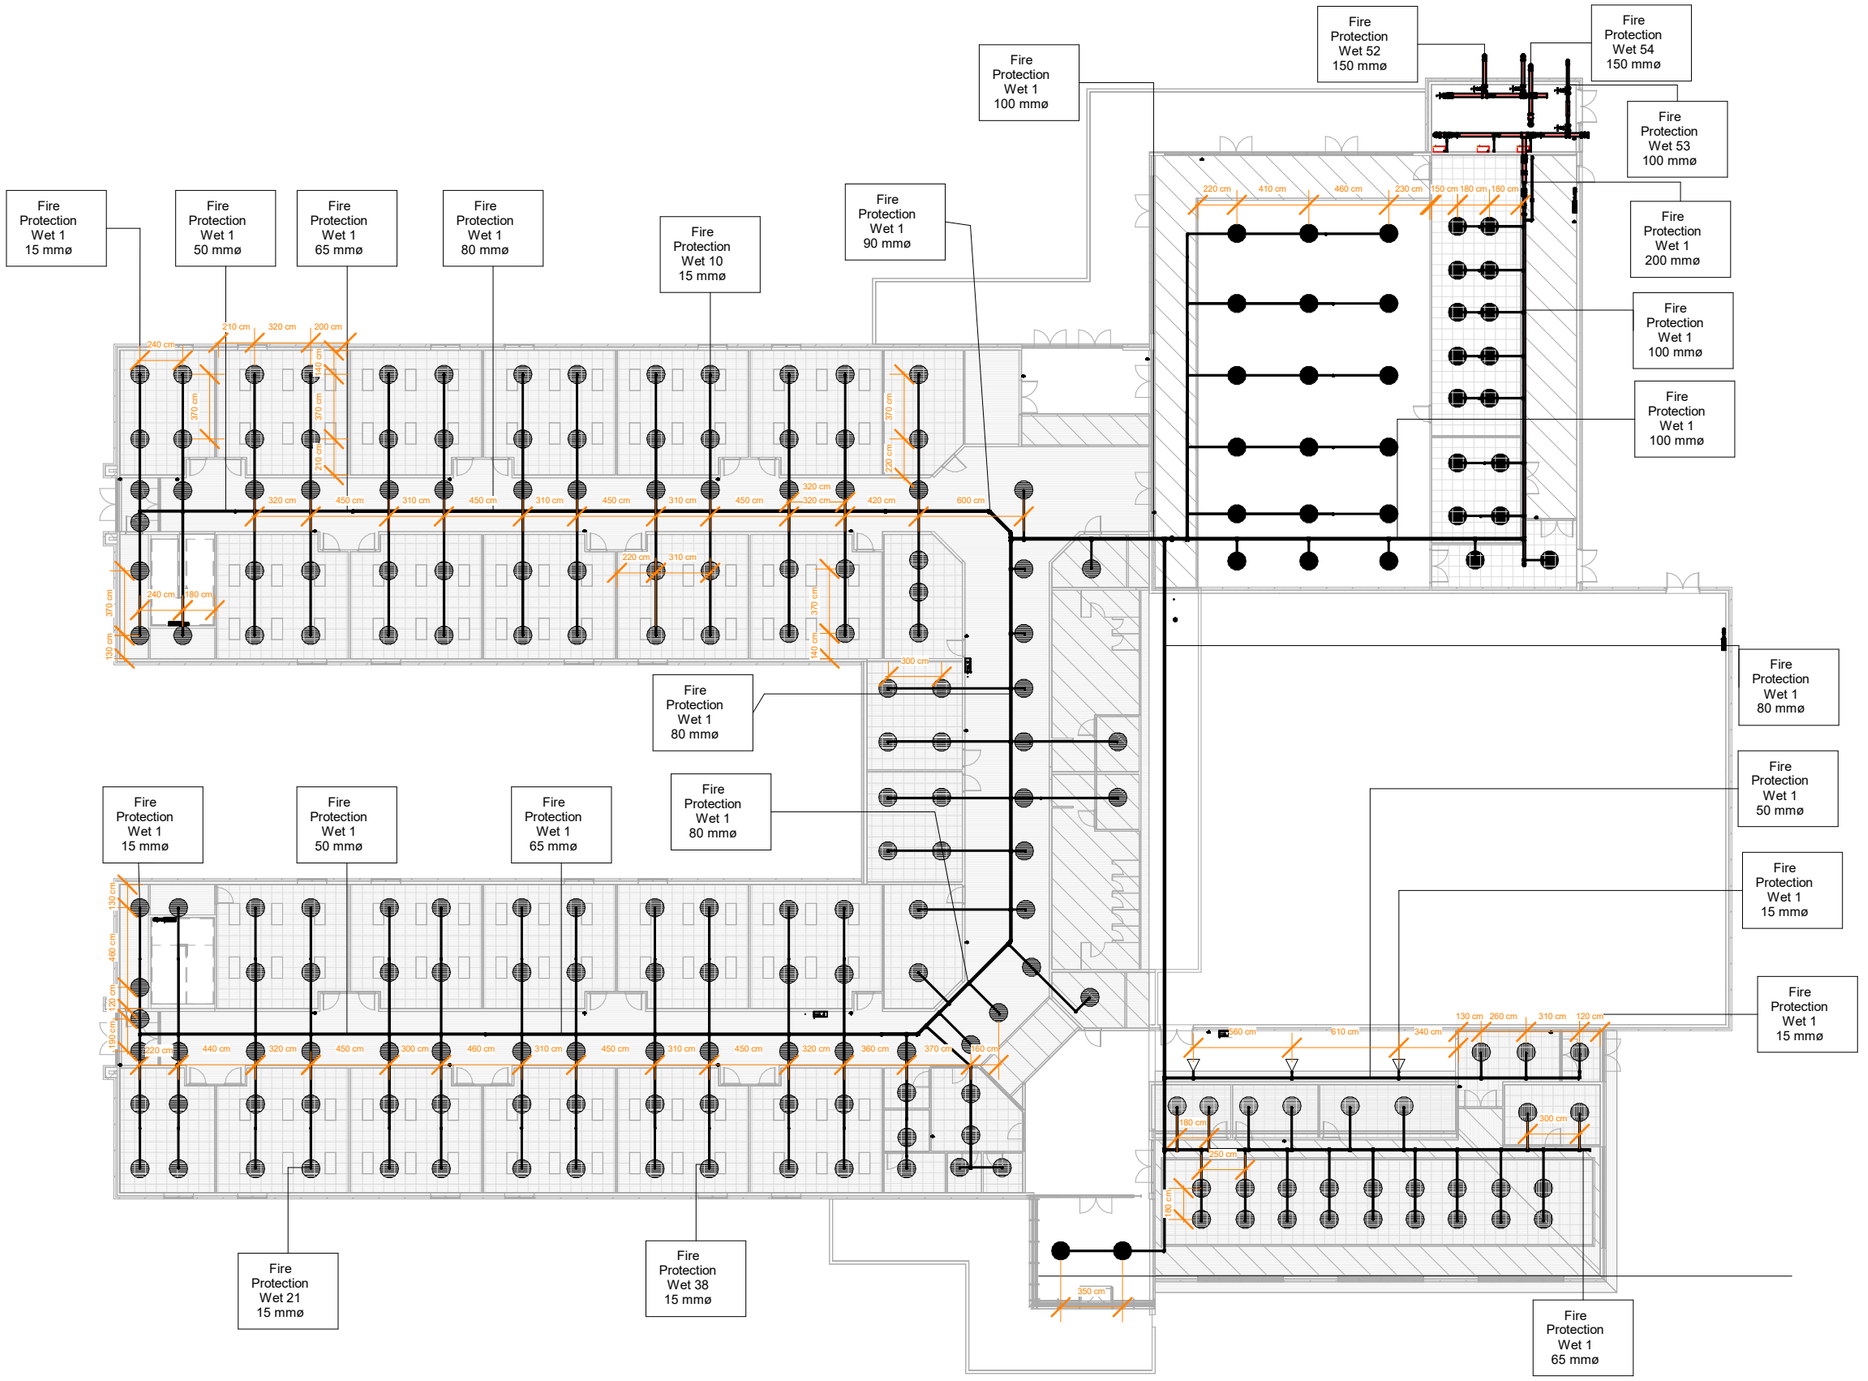

Hose Reel

Hose Rack

Jockey Pump

Fire Control Panle

Extinguisher

Pendent Sprinkel

Up right Sprinkel

Side Wall Sprinkel

OS&Y Valve

Reilef Valve

Team Members:

Omar Soliman
Kareem Tarek
Mahmoud Abdelmawla
Mariem Mohamed
Menna Nasser

Owner : WYZ


Project Name : Cairo School


level 1- Firefighting (1)

Project number	1
Date	16-oct-2026
Drawn by	OK&3M
Checked by	WYZ
Scale	As indicated


A-201

10/15/2026 2:44:28 PM

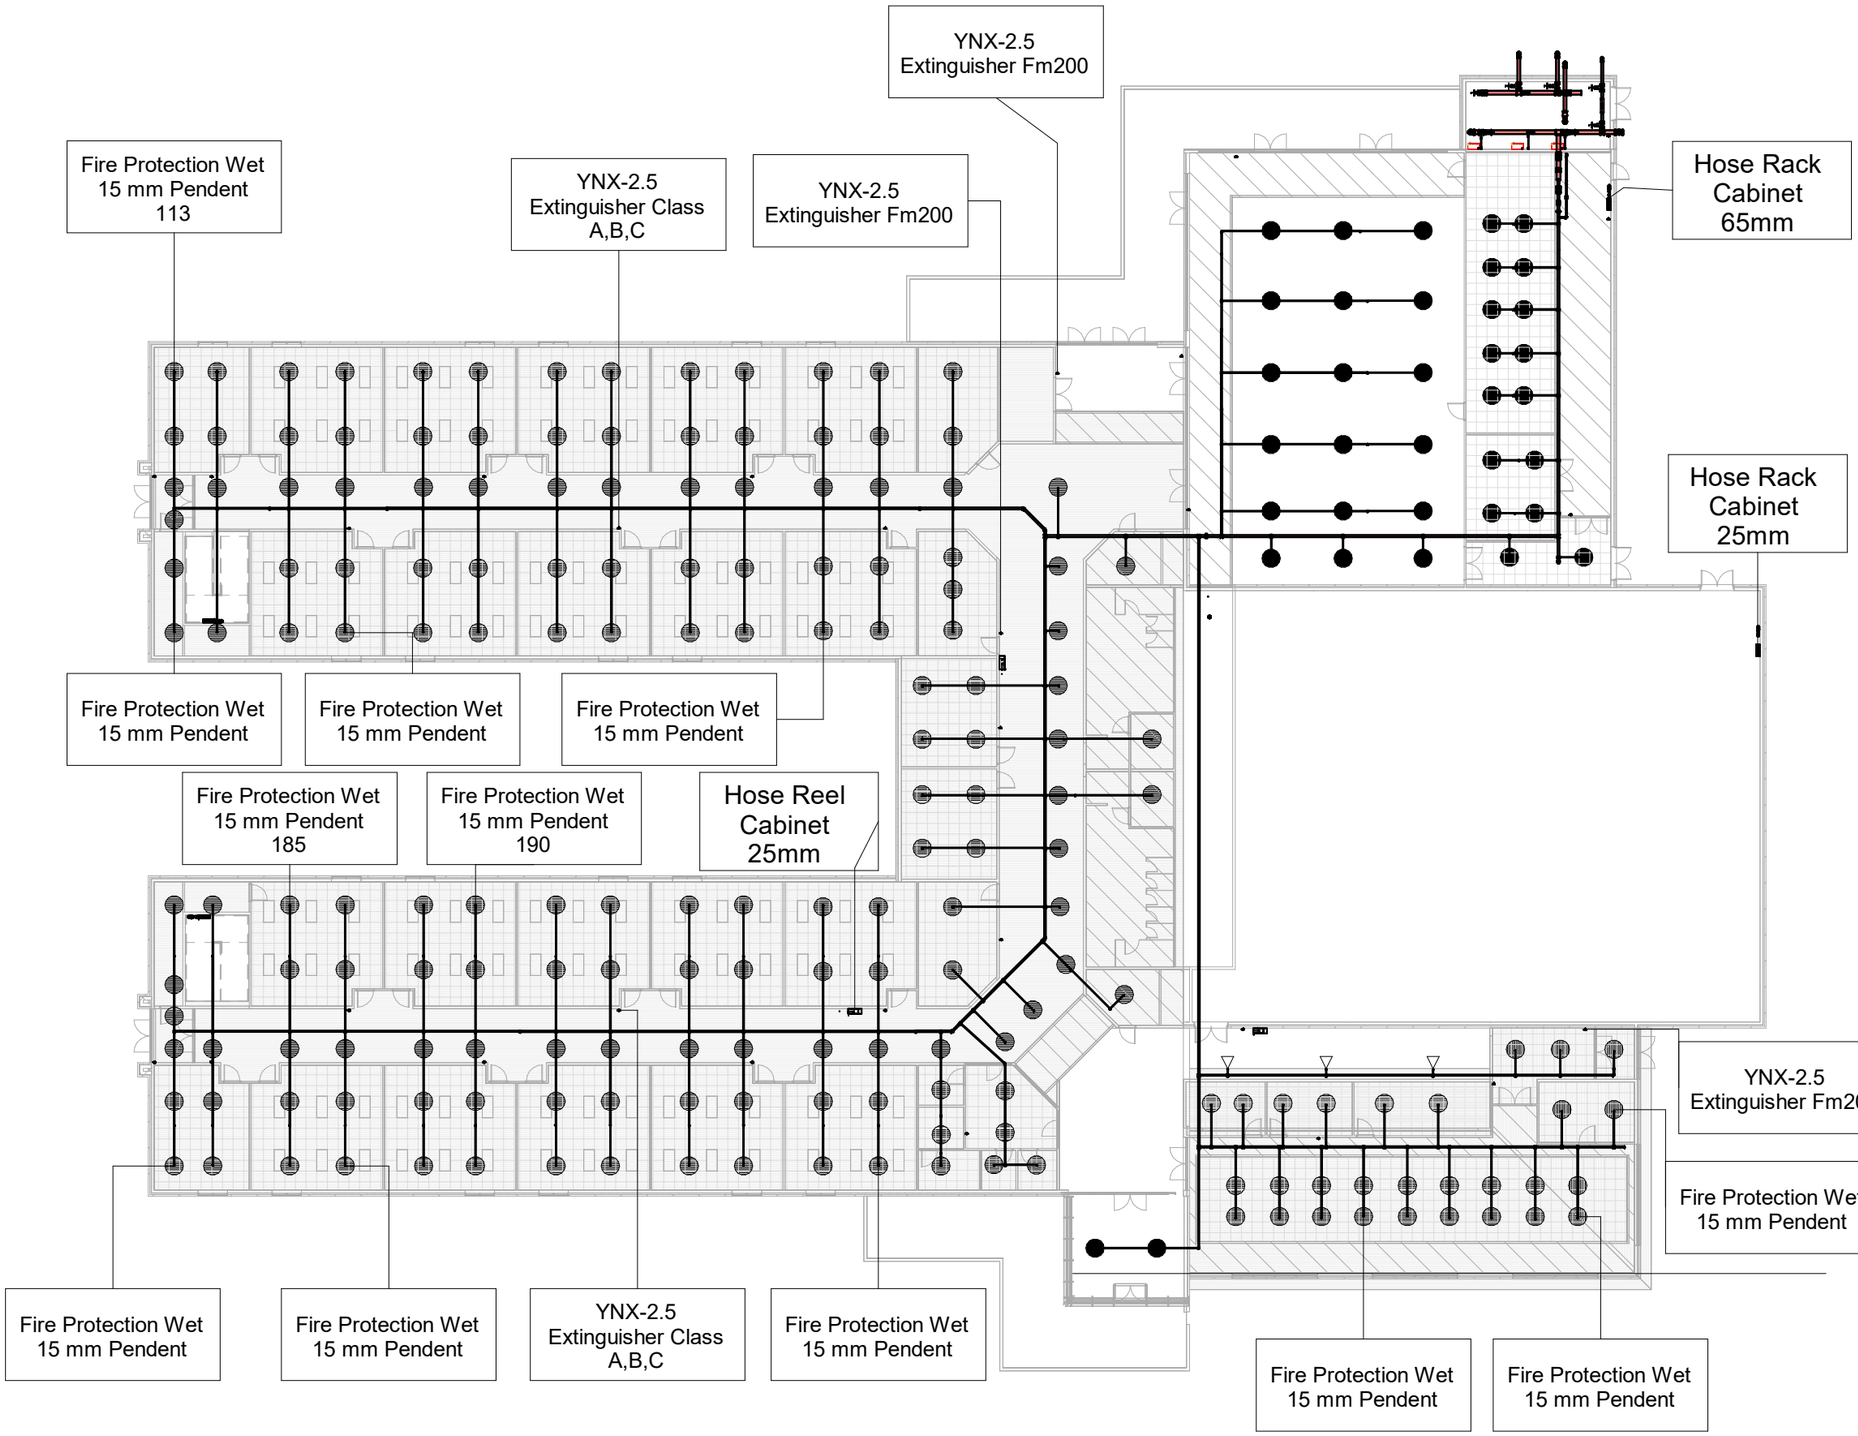


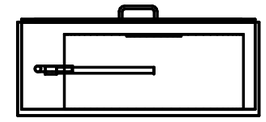


Hose Reel

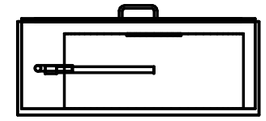

Hose Rack

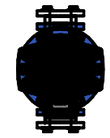

Jockey Pump

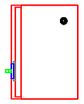

Fire Control Panle



Extinguisher


Pendent Sprinkel

Up right Sprinkel

Side Wall Sprinkel



OS&Y Valve

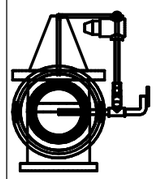

Reilef Valve

Team Members:

Omar Soliman
Kareem Tarek
Mahmoud Abdelmawla
Mariem Mohamed
Menna Nasser

Owner : WYZ


Project Name : Cairo School


level 1- Firefighting (2)

Project number	1
Date	16-oct-2026
Drawn by	OK&3M
Checked by	WYZ
Scale	As indicated


A-204

10/15/2026 5:52:30 PM

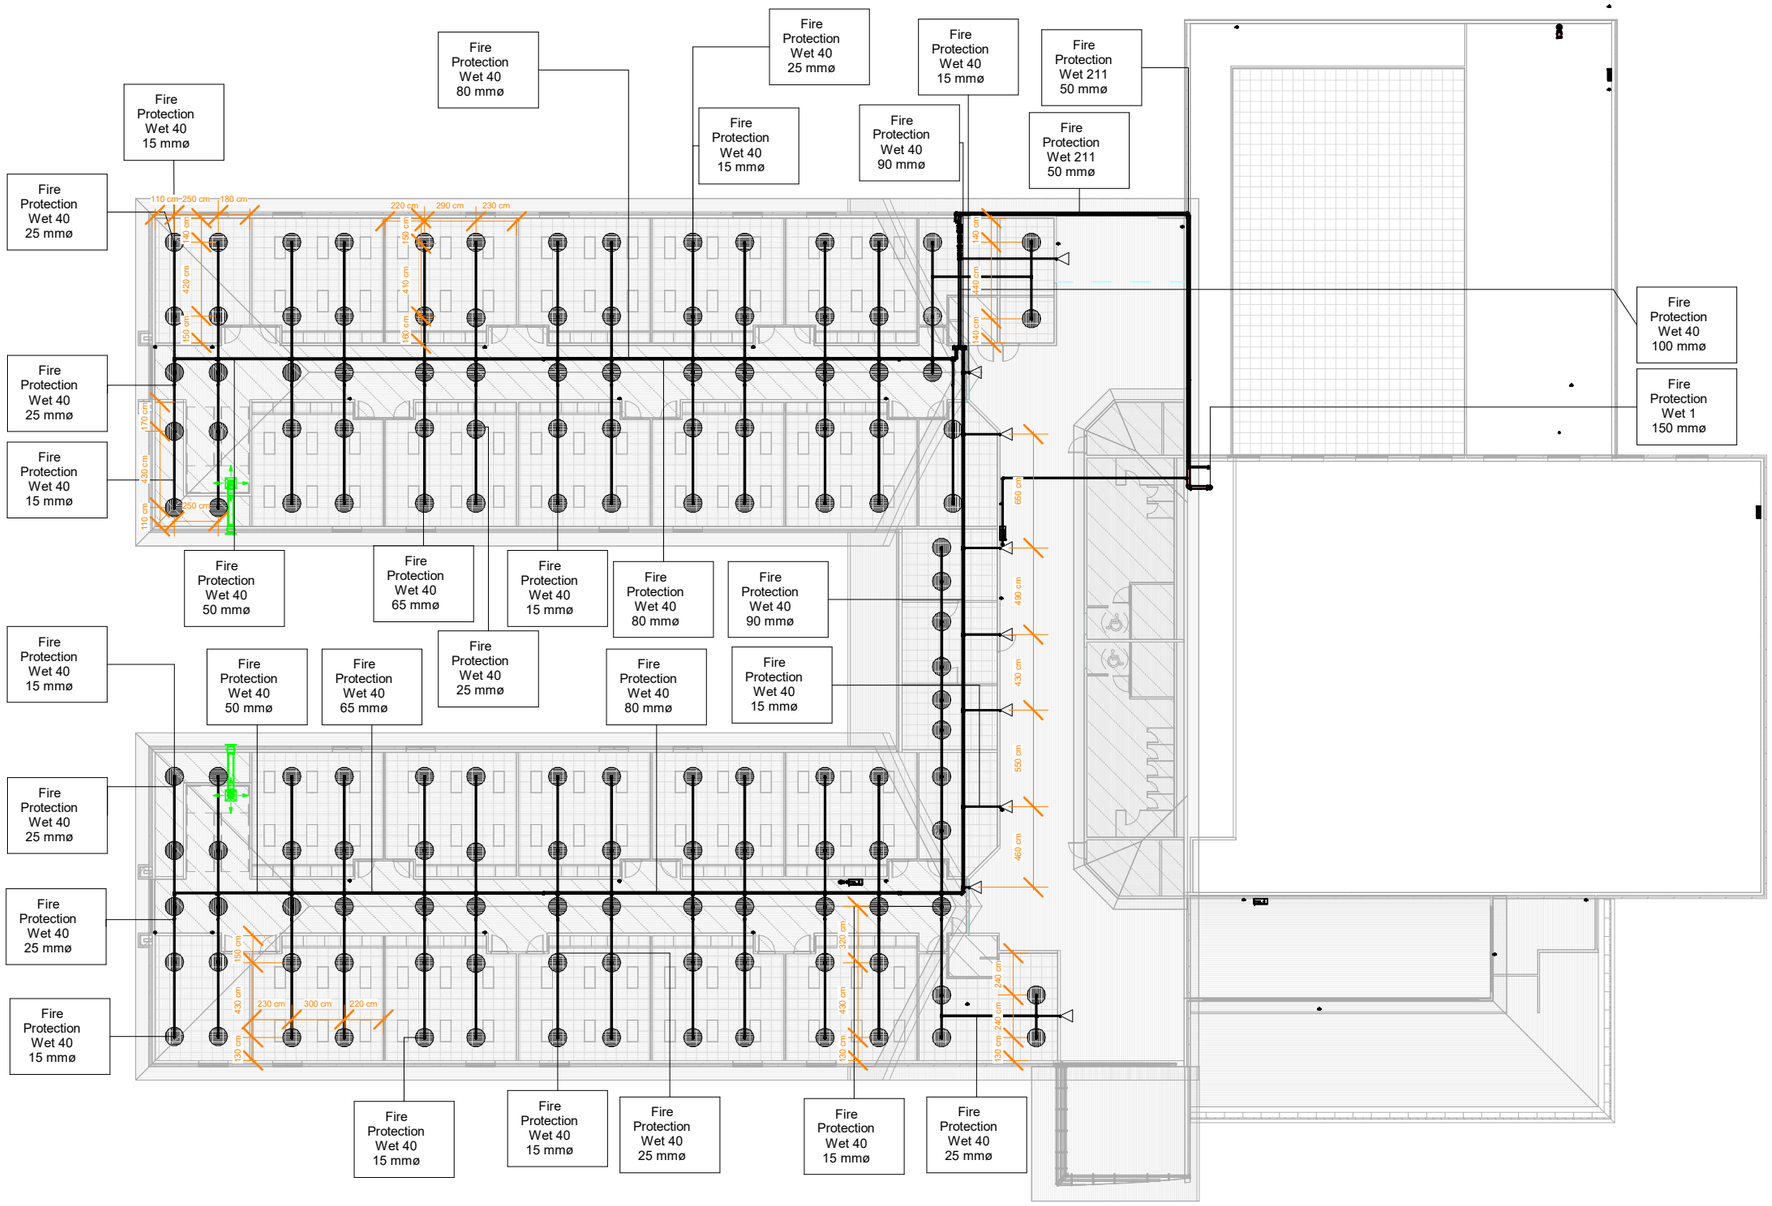

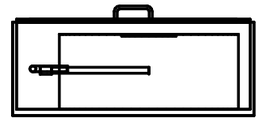


Hose Reel

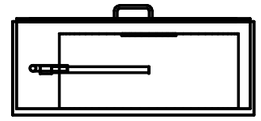

Hose Rack



Jockey Pump

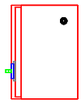

Fire Control Panle



Extinguisher


Pendent Sprinkel

Up right Sprinkel

Side Wall Sprinkel



OS&Y Valve

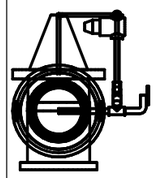

Reilef Valve



Team Members:

Omar Soliman
Kareem Tarek
Mahmoud Abdelmawla
Mariem Mohamed
Menna Nasser

Owner : WYZ

Project Name : Cairo School


level 2- Firefighting (1)


Project number	1
Date	16-oct-2026
Drawn by	OK&3M
Checked by	WYZ


A-202

Scale: As indicated


10/15/2026 4:12:57 PM

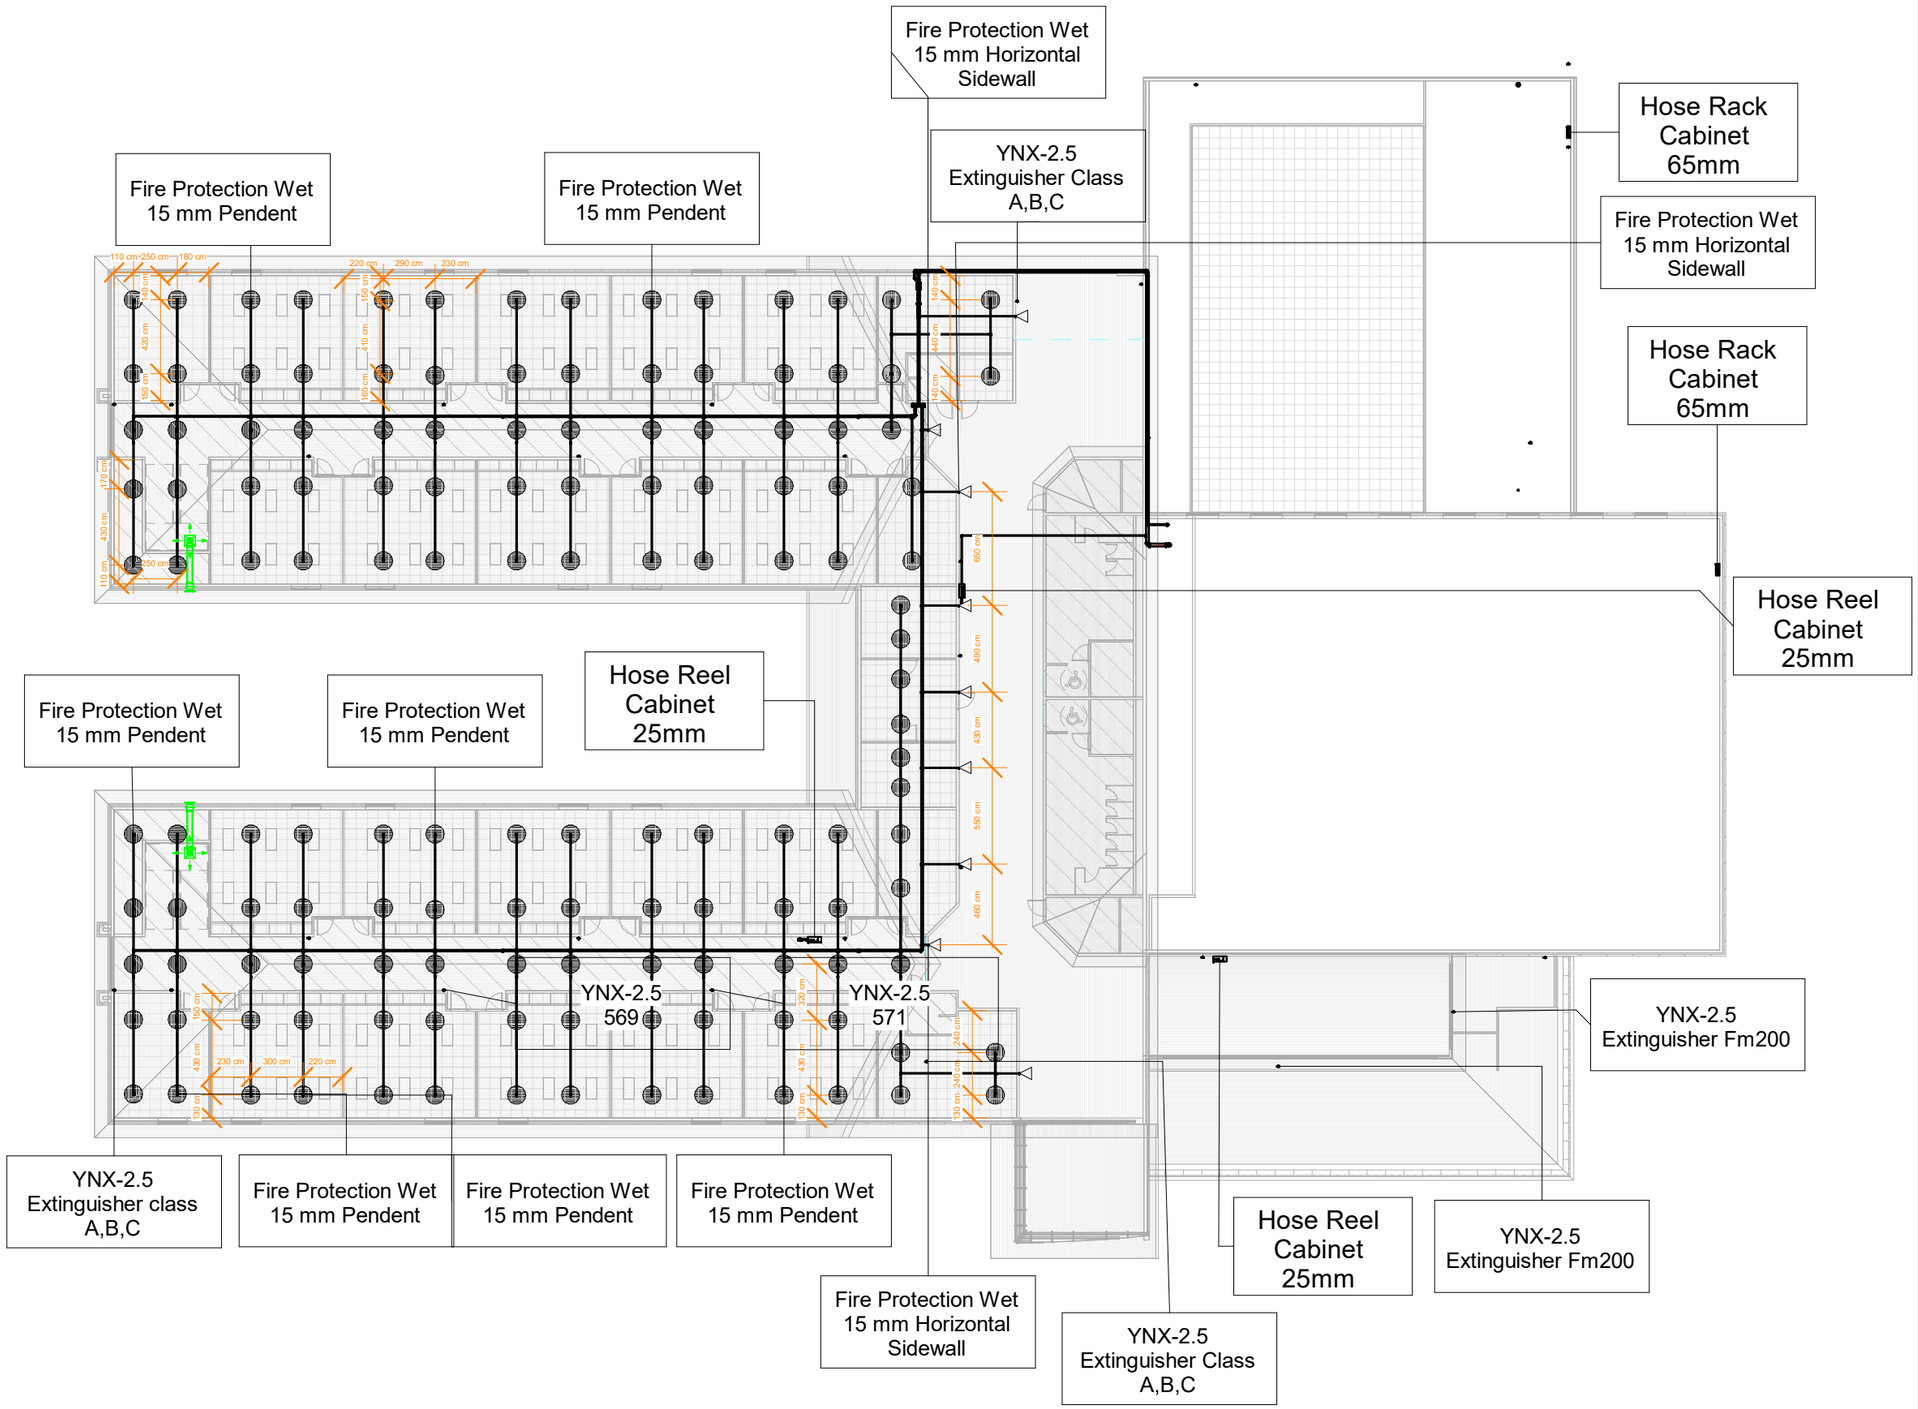

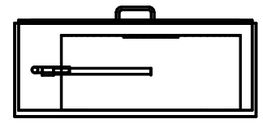
Hose Reel

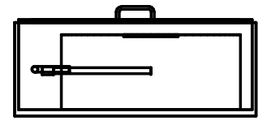
Hose Rack


Jockey Pump

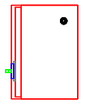
Fire Control Panle



Extinguisher

Pendent Sprinkel

Up right Sprinkel

Side Wall Sprinkel


OS&Y Valve

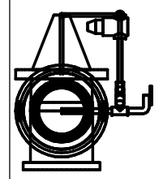
Reilef Valve

Team Members:

Omar Soliman
Kareem Tarek
Mahmoud Abdelmawla
Mariem Mohamed
Menna Nasser

Owner : WYZ

Project Name : Cairo School


level 2- Firefighting (2)


Project number	1
Date	16-oct-2026
Drawn by	OK&3M
Checked by	WYZ


A-203


Scale: As indicated

10/15/2026 8:39:47 PM

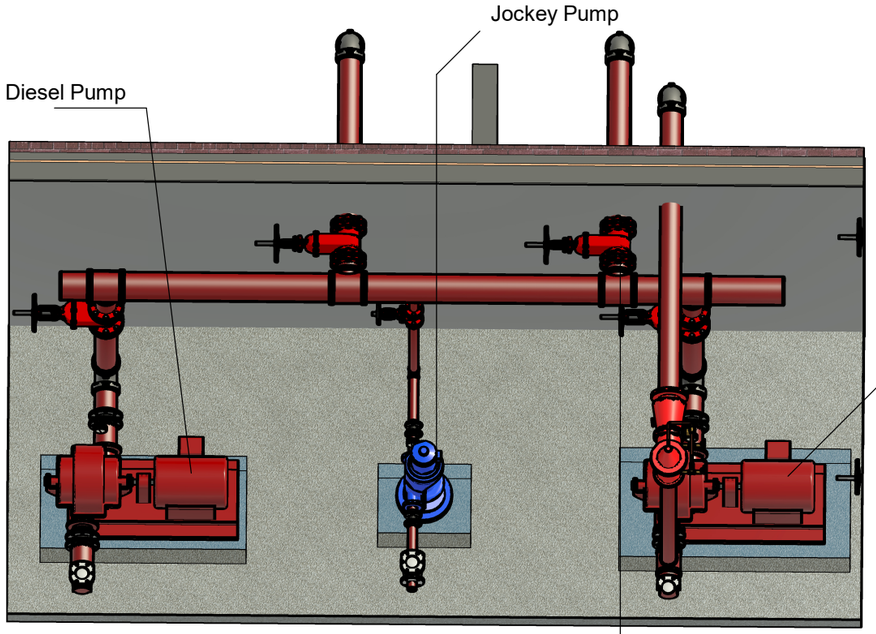


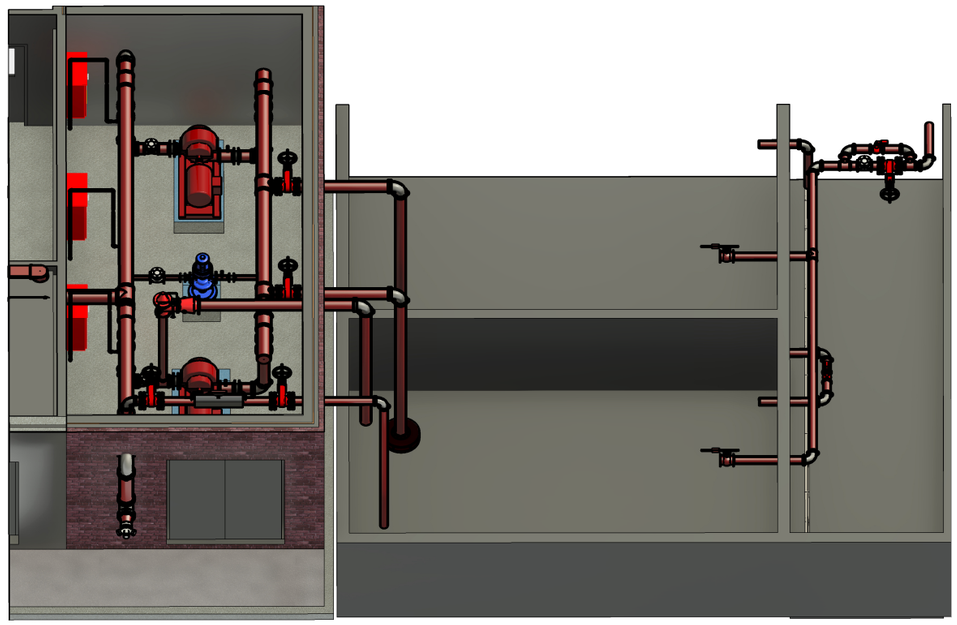

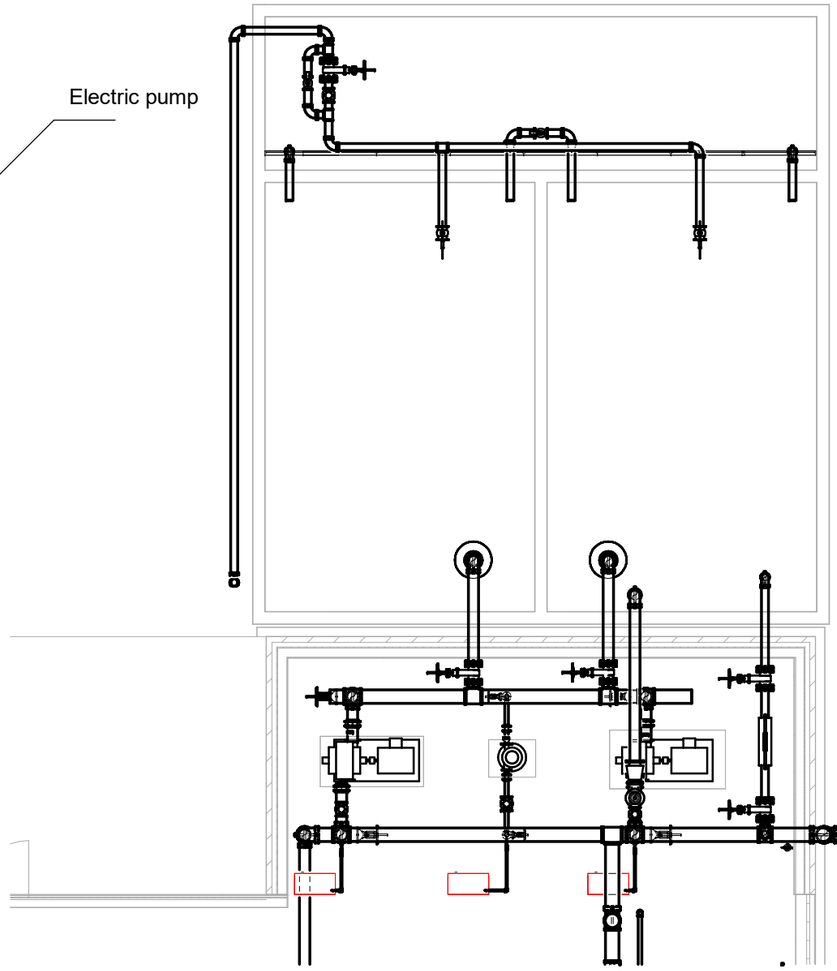

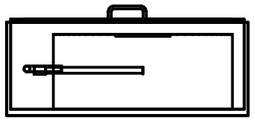


Hose Reel

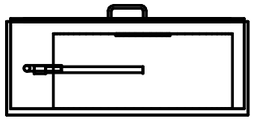

Hose Rack



Jockey Pump

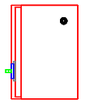

Fire Control Panle




Extinguisher


Pendent Sprinkel

Up right Sprinkel

Side Wall Sprinkel

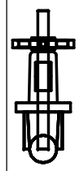

OS&Y Valve

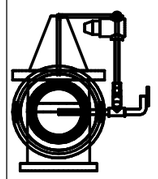

Reilef Valve

Team Members:

Omar Soliman
Kareem Tarek
Mahmoud Abdelmawla
Mariem Mohamed
Menna Nasser

Owner : WYZ

Project Name : Cairo School


Fire fighting 3D


Project number	1
Date	16-oct-2026
Drawn by	OK&3M
Checked by	WYZ


A-205

Scale: As indicated


10/15/2026 7:47:44 PM

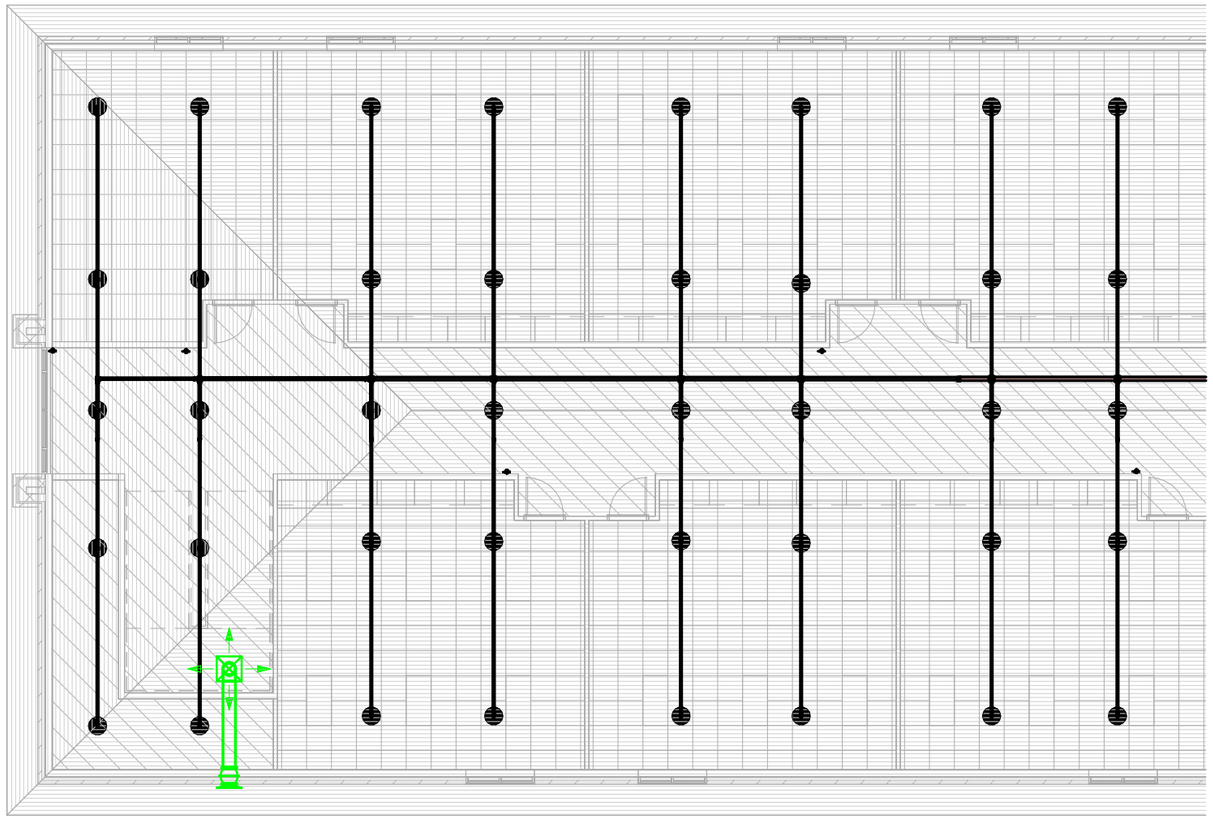

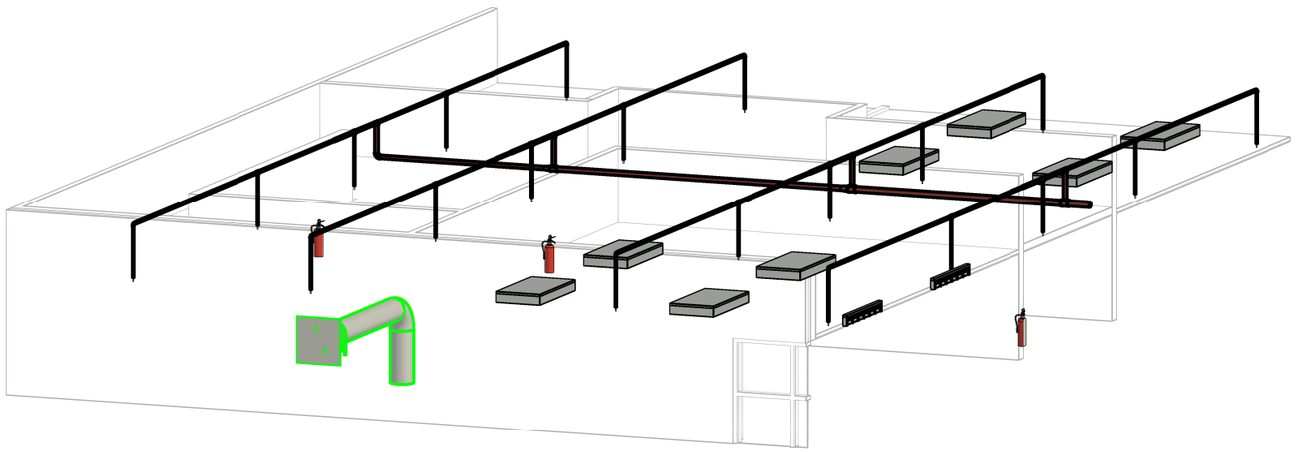

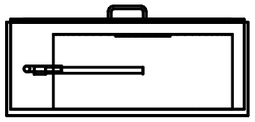


Hose Reel

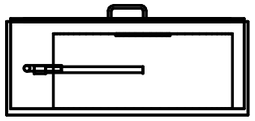

Hose Rack



Jockey Pump

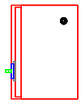

Fire Control Panle



Extinguisher


Pendent Sprinkel

Up right Sprinkel

Side Wall Sprinkel



OS&Y Valve

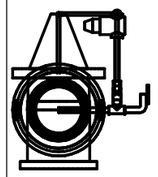

Reilef Valve

Team Members:

Omar Soliman
Kareem Tarek
Mahmoud Abdelmawla
Mariem Mohamed
Menna Nasser

Owner : WYZ


Project Name : Cairo School

X-CLIP


Project number	1
Date	16-oct-2026
Drawn by	OK&3M
Checked by	WYZ
Scale	As indicated

A-208


10/15/2026 8:46:16 PM

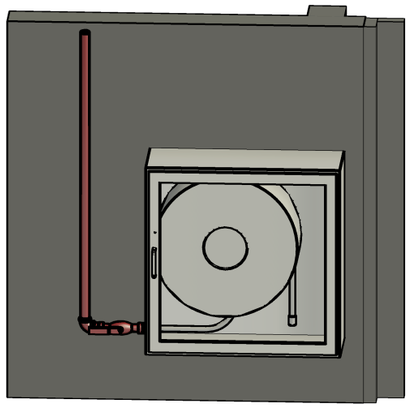


HOSE REEL

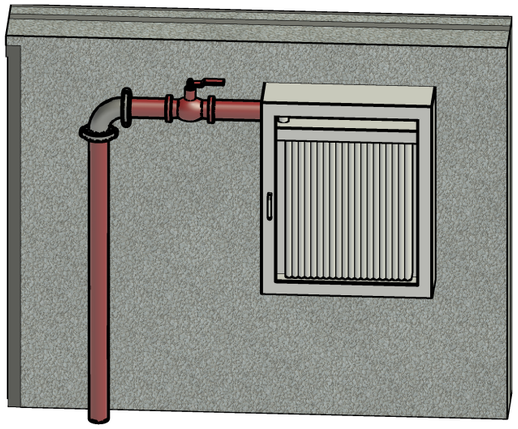


HOSE RACK

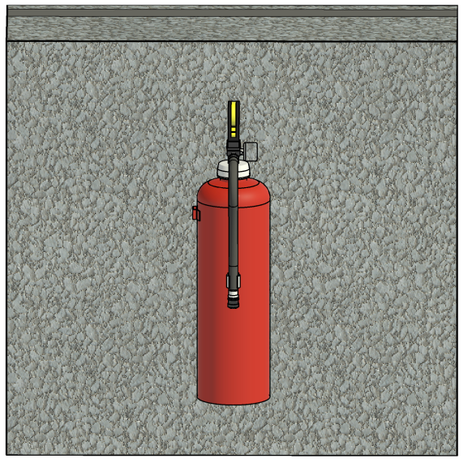


EXTINGUISHER

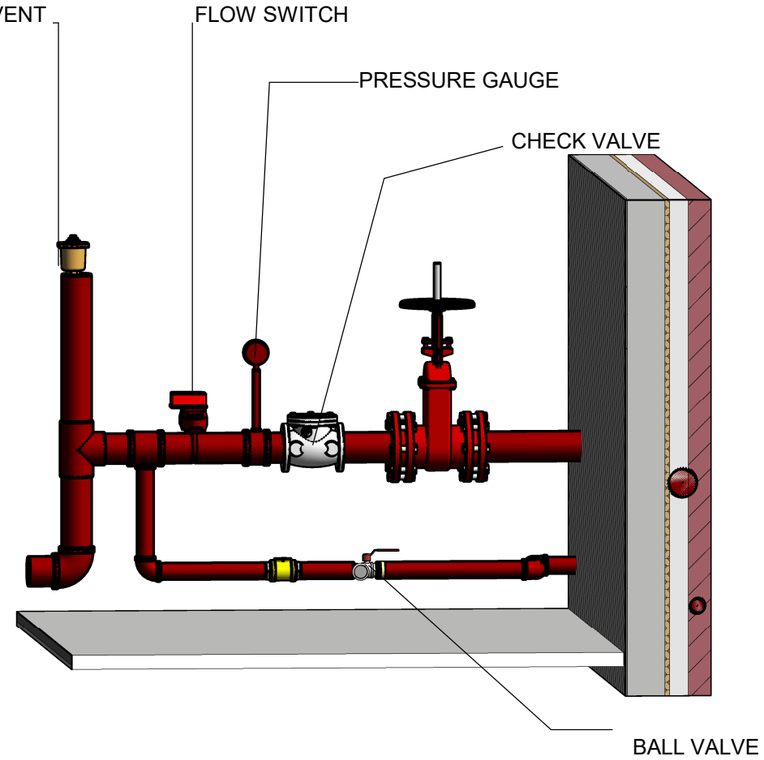


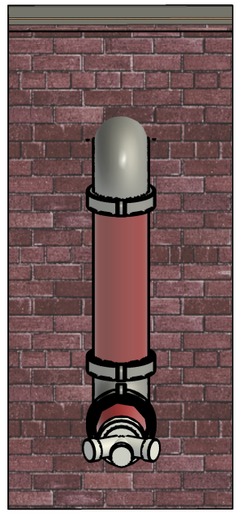

SIAMESE CONNECTION

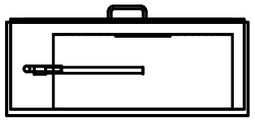


Hose Reel

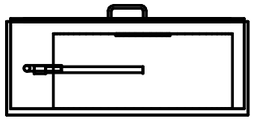

Hose Rack



Jockey Pump

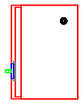

Fire Control Panle



Extinguisher


Pendent Sprinkel

Up right Sprinkel

Side Wall Sprinkel



OS&Y Valve

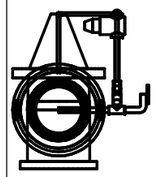

Reilef Valve

Team Members:

Omar Soliman
Kareem Tarek
Mahmoud Abdelmawla
Mariem Mohamed
Menna Nasser

Owner : WYZ

Project Name : Cairo School

Fire fighting 3D

Project number	1
Date	16-oct-2026
Drawn by	OK&3M
Checked by	WYZ
Scale	1 : 20

A-206

10/15/2026 8:34:39 PM